




Hélène GREBEAUVALL
Architecte d'intérieur - Freelance



« Rien de grand dans le monde ne s'est
accompli sans passion. »

Hegel

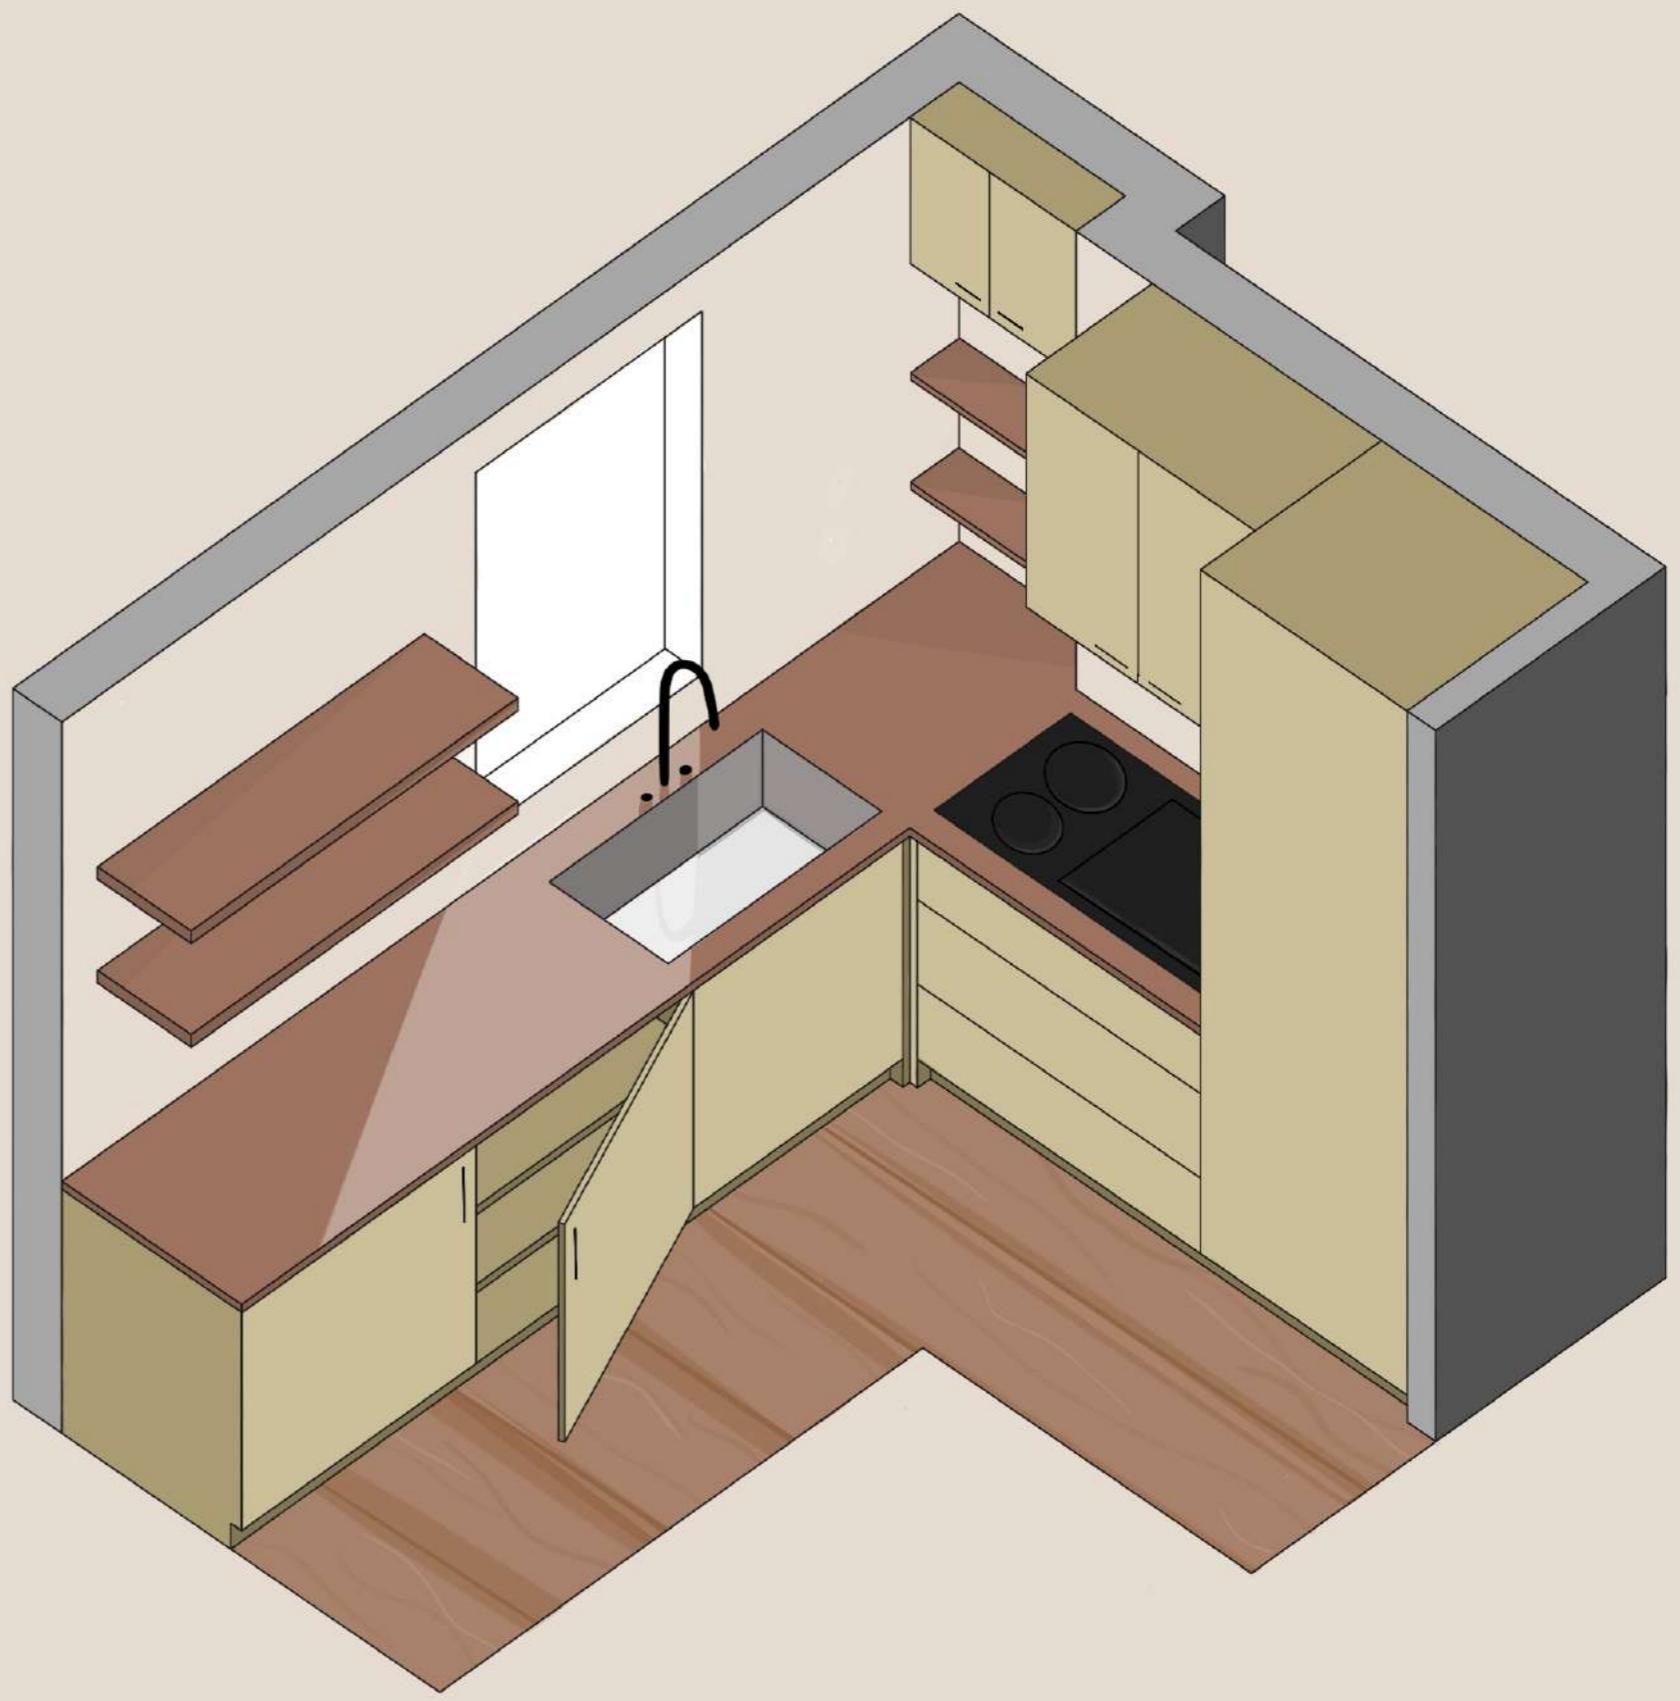

SOMMAIRE

01. **A propos**

Découvrez mon parcours, mes valeurs et mon approche en tant qu'architecte d'intérieur, maître d'oeuvre et designer.

02. **Services proposés**

Explorez les services sur mesure que je propose aux particuliers et aux professionnels, de la conception à la réalisation.

03. **Portfolio**

Une sélection de mes projets : des réalisations variées, allant des résidences privées aux espaces commerciaux, en passant par du design.

04. **Processus de travail**


Mon approche détaillée pour assurer le succès de chaque projet, de la conception initiale au suivi de chantier.

05. **Témoignages**

Avis et retours d'expérience de mes clients et entreprises.

06. **Contact**

Pour toute demande, projet ou collaboration, contactez-moi.

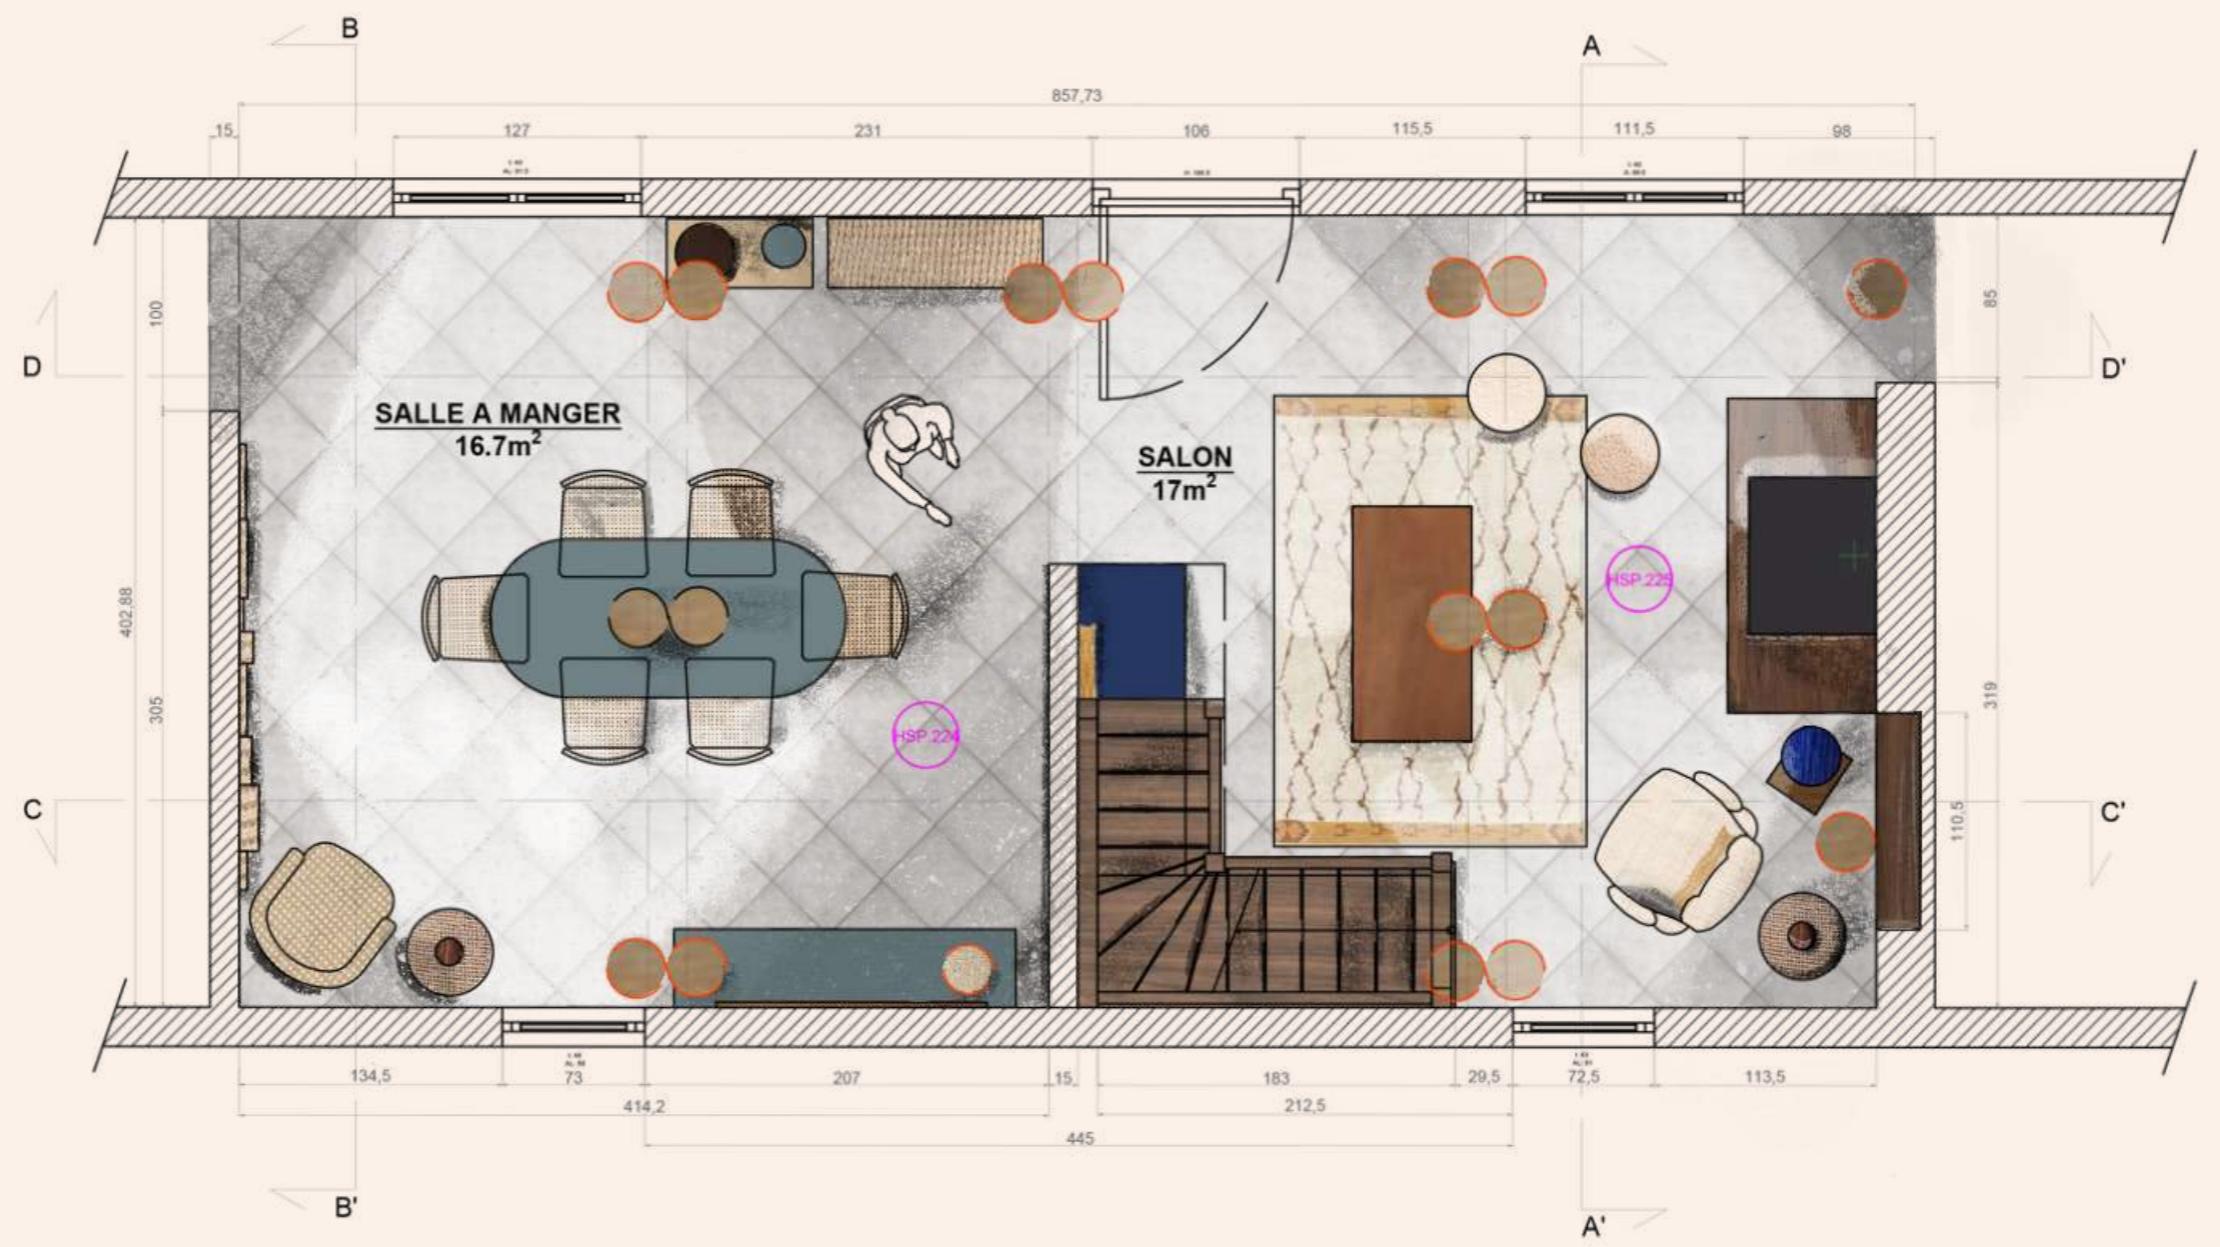

A PROPOS

Hélène GREBEAUVAL – Architecte d'Intérieur, Maître d'Œuvre & Designer

LNArchi est une agence spécialisée dans la conception d'espaces intérieurs, la rénovation et la maîtrise d'œuvre, que j'ai fondée afin de donner vie à des projets alliant esthétique, fonctionnalité et singularité.

À travers LNArchi, j'accompagne mes clients dans la transformation de leurs espaces, en conciliant créativité et rigueur technique.








Mon parcours, marqué par une formation en design global à l'École de Design Nantes Atlantique, puis un master en architecture d'intérieur à LISAA, m'a permis d'acquérir une vision intégrale du métier. Cette approche multidisciplinaire me permet d'intervenir aussi bien en conception qu'en suivi de chantier, afin de garantir une réalisation fidèle aux attentes de chaque projet.

Forte d'expériences en France et à l'international, j'ai eu l'opportunité de collaborer avec des enseignes renommées ainsi que des clients particuliers exigeants, souhaitant des projets sur mesure et haut de gamme. J'ai travaillé sur des réalisations variées, allant du résidentiel aux espaces professionnels et commerciaux.

Cette diversité nourrit mon approche et me permet de proposer des solutions uniques, adaptées aux besoins et aux usages de chaque client.

En parallèle de mon travail au sein de LNArchi, j'interviens également en freelance pour des agences d'architecture et de design, apportant mon expertise sur des missions spécifiques ou en sous-traitance.

Mon engagement est de fournir des solutions sur-mesure, alliant fonctionnalité, esthétique et efficacité avec un suivi rigoureux, de la conception à la livraison.

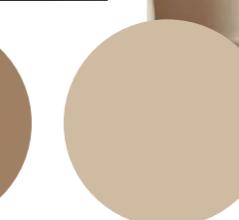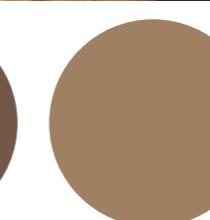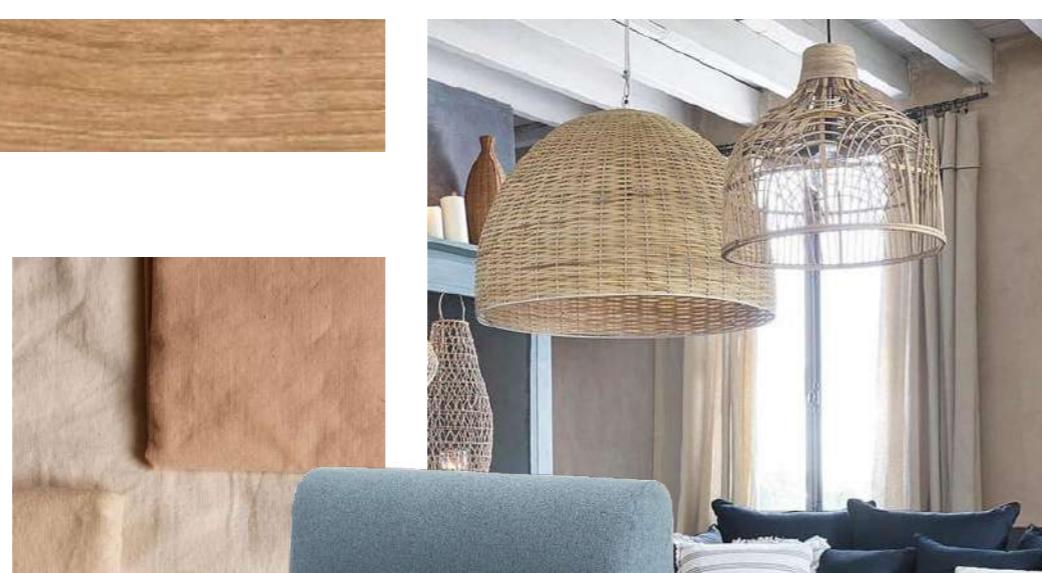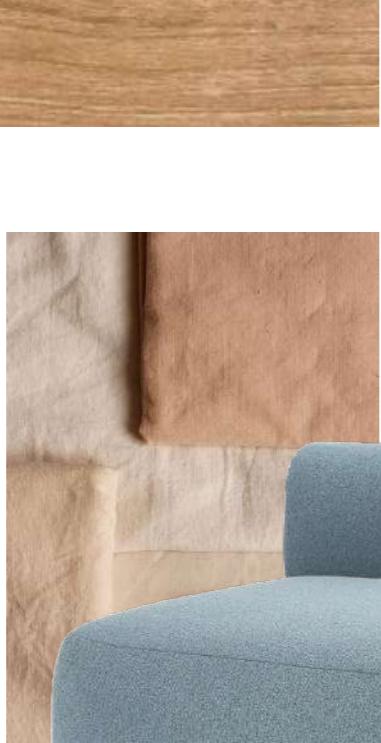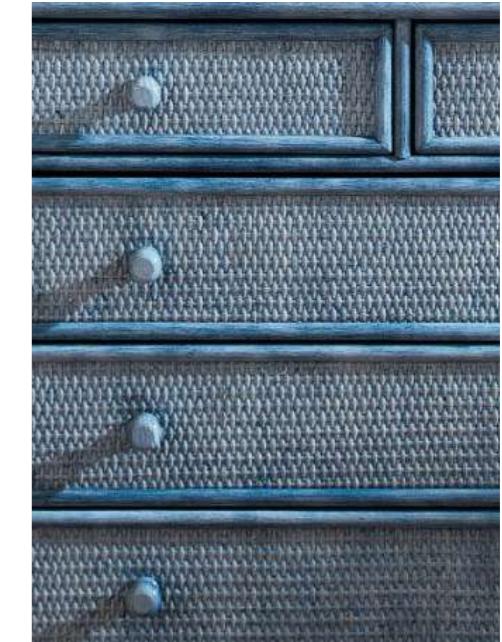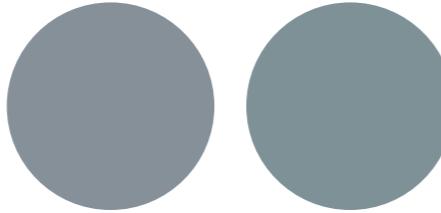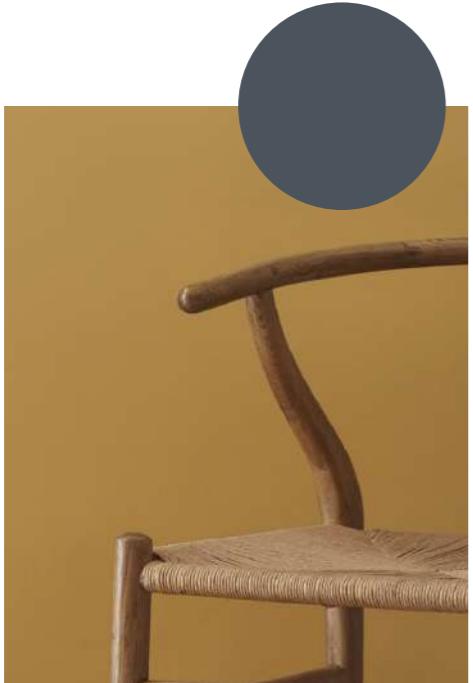

SERVICES PROPOSÉS

LNArchi offre une gamme de services sur-mesure, alliant créativité, fonctionnalité et expertise technique. Que vous soyez particulier ou professionnel, je vous accompagne à chaque étape de votre projet, de la conception à la réalisation.

Pour les particuliers

Aménagement intérieur : Conception et optimisation des espaces.

Rénovation : Modernisation et réorganisation des lieux.

Optimisation de l'espace : Maximisation des surfaces.

Cuisines & salles de bain : Design et agencement fonctionnel.

Suivi de chantier : Coordination et gestion des travaux.

Pour les professionnels

Espaces de travail : Aménagement optimisé des bureaux.

Design commercial : Création d'ambiances attractives.

Optimisation des espaces : Ergonomie et circulation améliorées.

Maîtrise d'œuvre : Pilotage global des projets.


En Freelance

Plans techniques : Élaboration détaillée.

Modélisation 3D : Visualisation réaliste.

Assistance technique : Suivi et coordination de projet.

Chaque projet est étudié avec rigueur pour des solutions adaptées et efficaces.

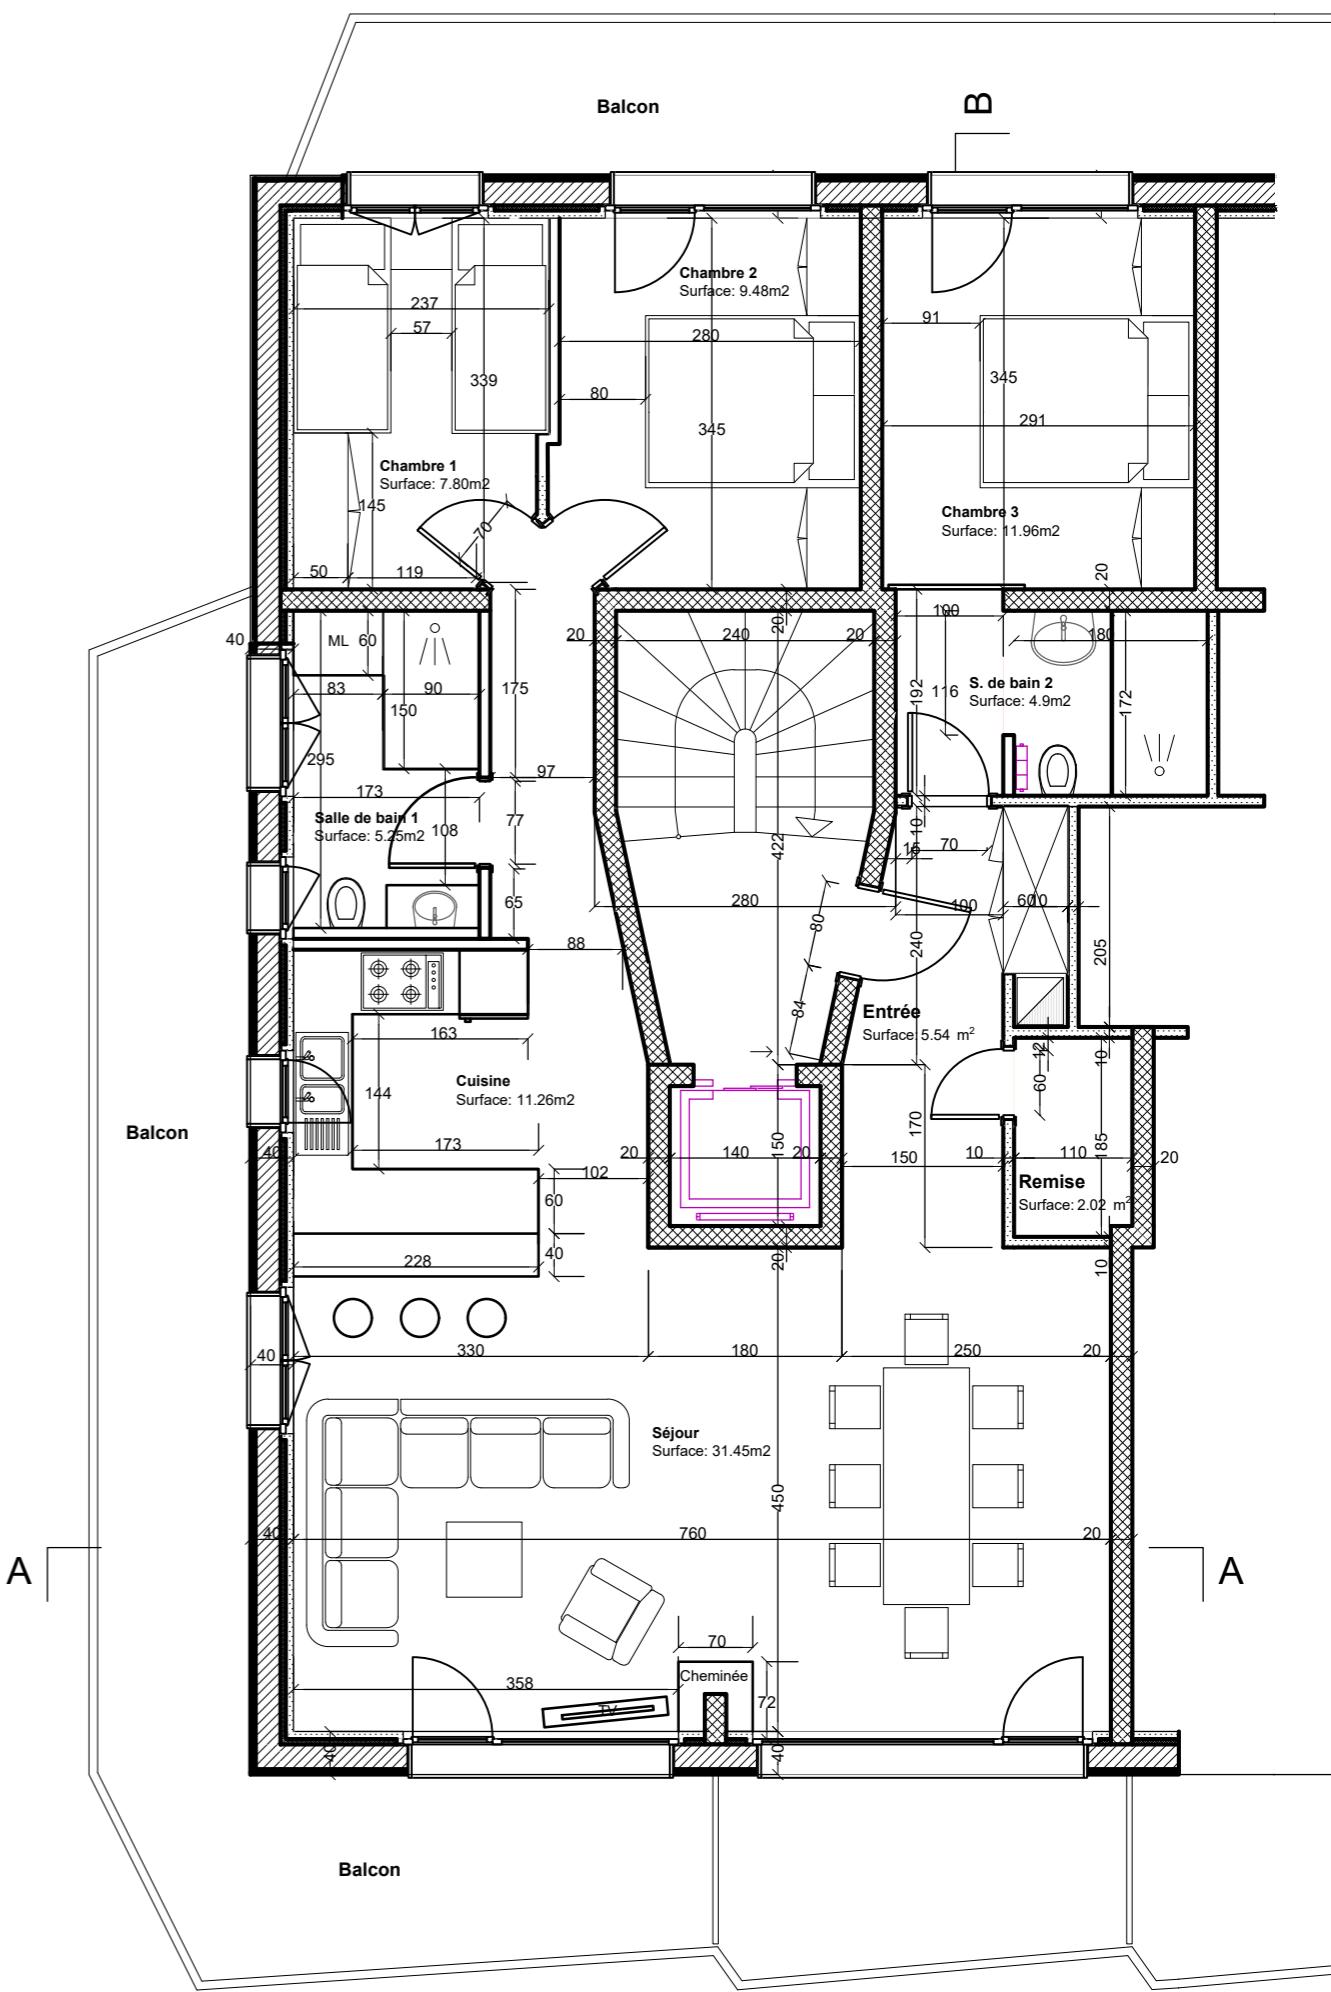

SOMMAIRE PROJETS CLIENTS PARTICULIERS

01. **Bras d'Or**

Rénovation énergétique du rez de chaussée d'une maison de campagne.

02. **Cocoon**

Aménagement optimisé d'une chambre parentale avec un dressing sur mesure.

03. **Renaissance**

Transformation d'un ancien relais de chasse en résidence secondaire.

04. **Épure**

Conception d'un meuble TV minimaliste dans un salon à personnaliser.

05. **Studio 16**

Transformation d'un studio parisien en optimisant chaque mètre carré.

06. **Au Fil des Marées**

Création d'une bibliothèque sur mesure dans une longère normande.


07. **Signature**


Conception et fabrication d'une collection de mobilier sur mesure.

Bras d'Or

Réalisation de l'agence LNArchî


Rafraîchissement et modernisation d'une maison de campagne de 100 m² en Normandie, avec un accent mis sur l'amélioration de son efficacité énergétique. L'isolation a été renforcée, les équipements mis aux normes, et les revêtements de sol modifiés pour apporter un nouveau souffle à l'espace. La mise en peinture a été réalisée pour moderniser l'ensemble, tout en conservant le mobilier existant pour maintenir une ambiance chaleureuse et accueillante.

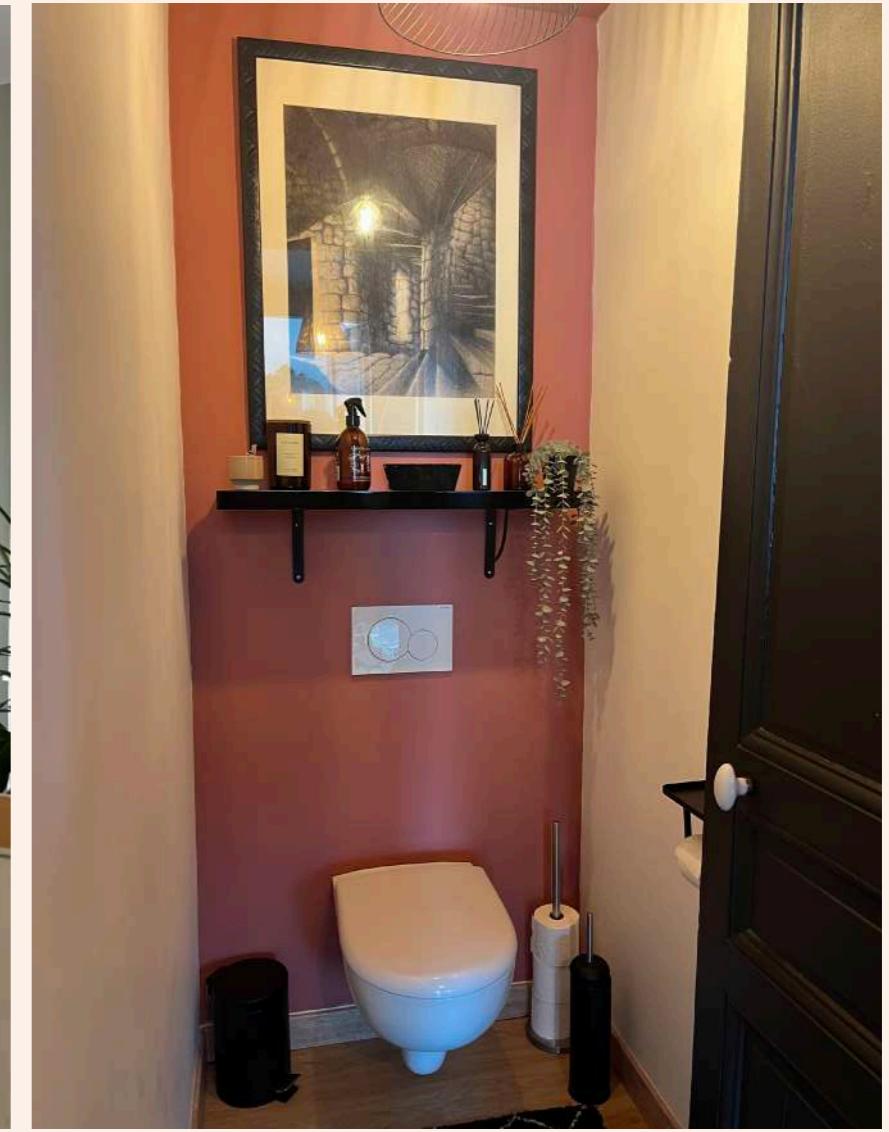

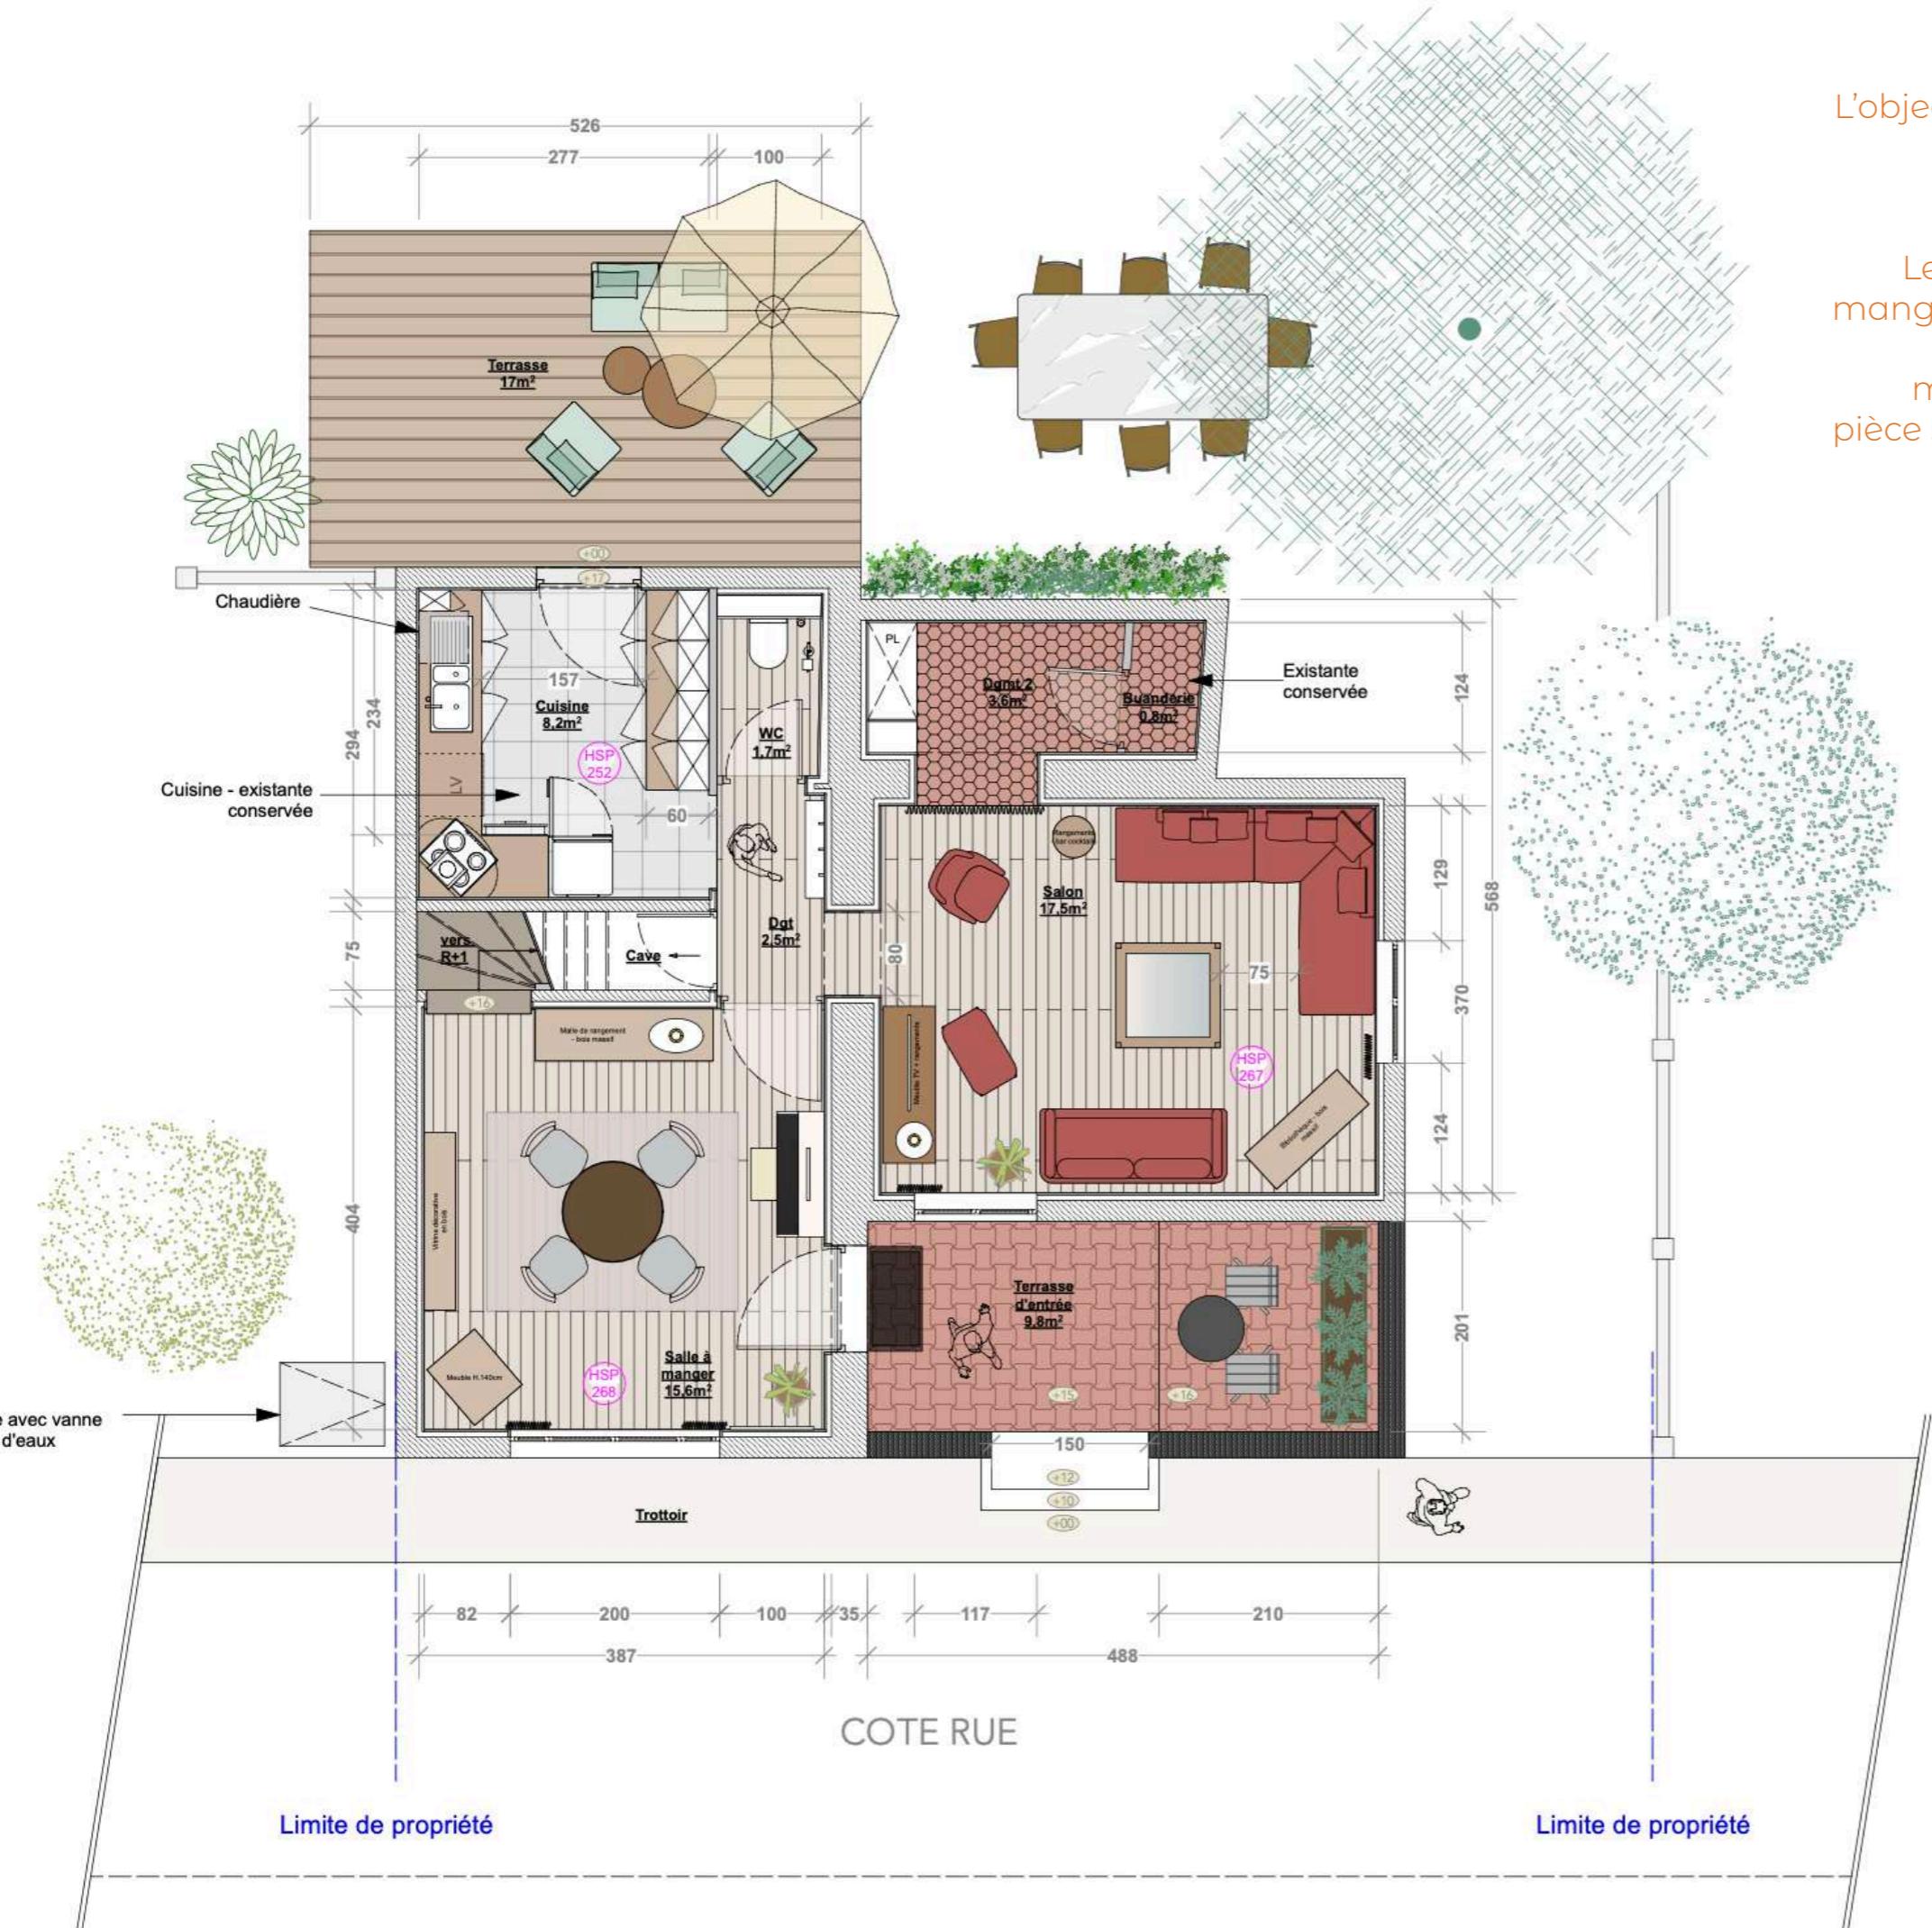

L'objectif était de créer un intérieur confortable, idéal pour recevoir, tout en optimisant l'agencement et l'utilisation de l'espace.

Le sas d'entrée, séparant le salon, la salle à manger et la cuisine (conservée), a été peint en noir sur les murs et le plafond pour marquer un contraste et donner à chaque pièce son propre univers. Les meubles existants de la cliente ont été intégrés avec soin.

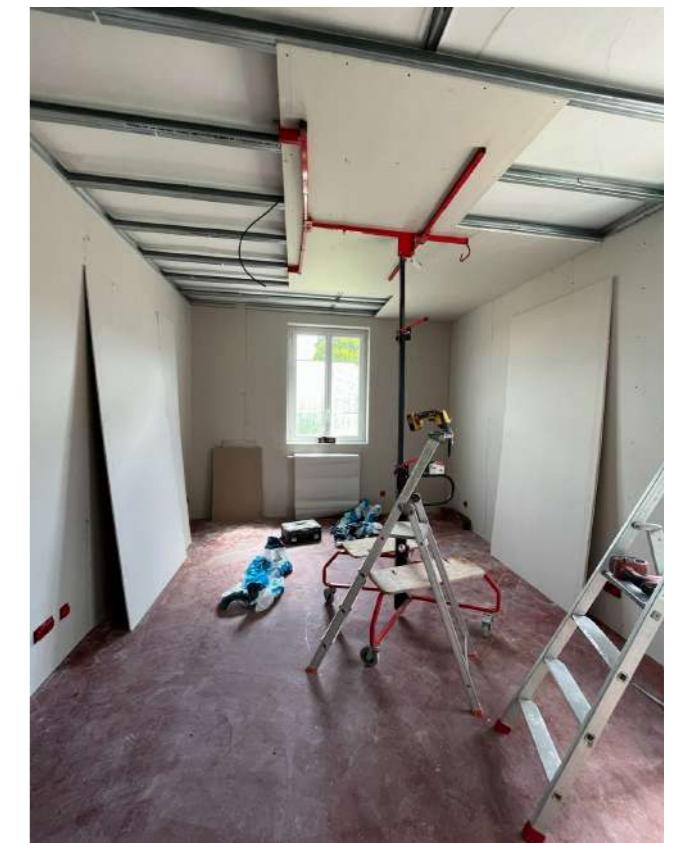


Les WC ont été modernisés et optimisés pour allier praticité et esthétique, tout en maintenant l'harmonie de l'ensemble.

Gocoon

Réalisé au sein de l'agence d'Alice Frebourg


Dans une maison de ville de 100 m², avec à l'étage une chambre parentale attenante à une salle d'eau ouverte, l'espace a été optimisé pour les futurs parents. Des rangements fermés ont été intégrés sur toute la hauteur du mur, offrant ainsi un maximum de stockage. La salle d'eau a été rafraîchie pour créer un environnement plus moderne et fonctionnel.

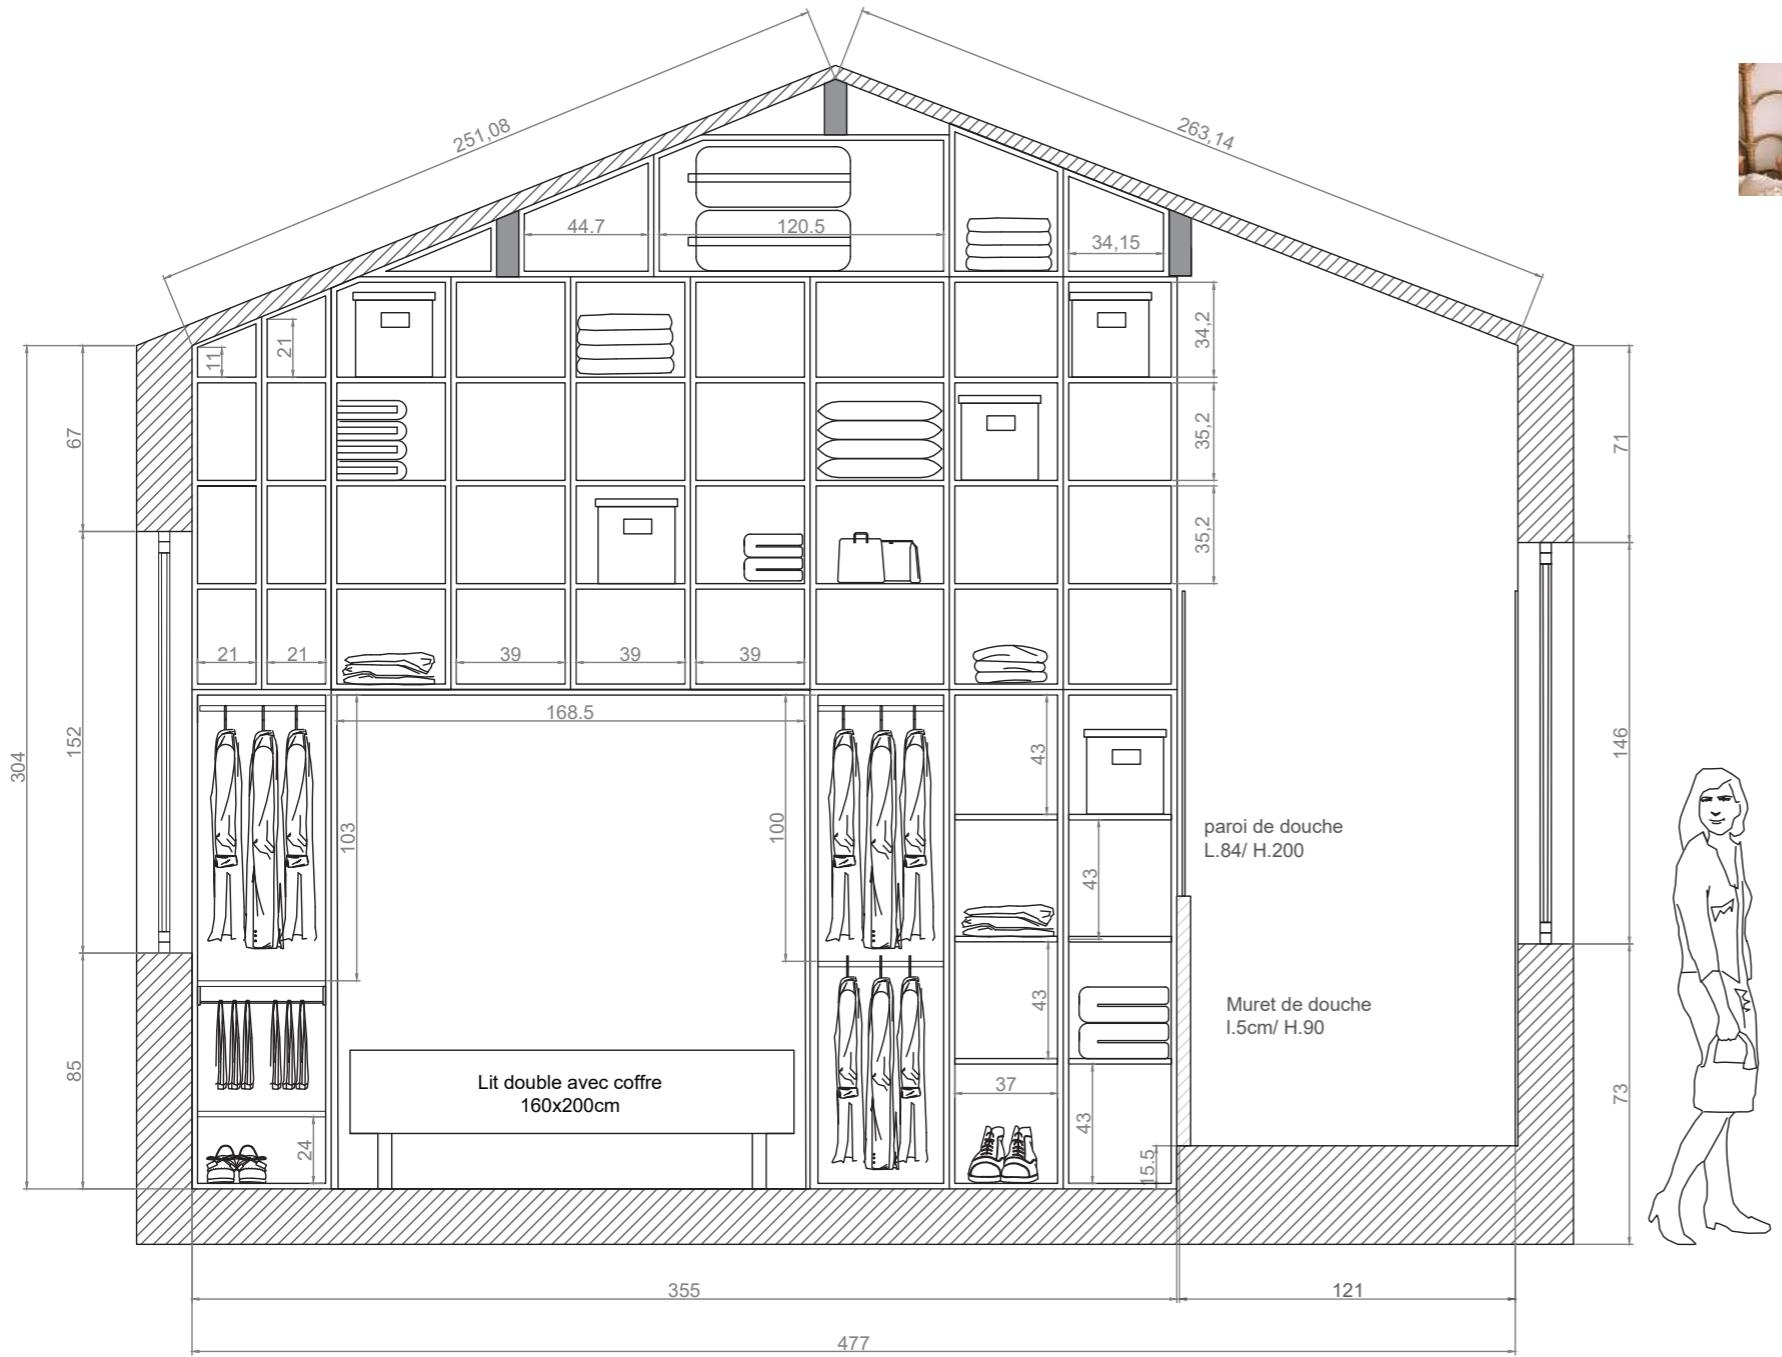



Pour compléter l'aménagement de la chambre parentale, une tête de lit sur mesure a été conçue avec des rangements fermés tout autour, permettant d'optimiser l'espace tout en préservant une esthétique épurée. Ces rangements offrent une solution de stockage discrète et fonctionnelle, idéale pour organiser les effets personnels des futurs parents.



Une échelle, également sur mesure, a été ajoutée pour faciliter l'accès aux compartiments hauts, offrant ainsi un confort supplémentaire tout en intégrant parfaitement le design global de la pièce.

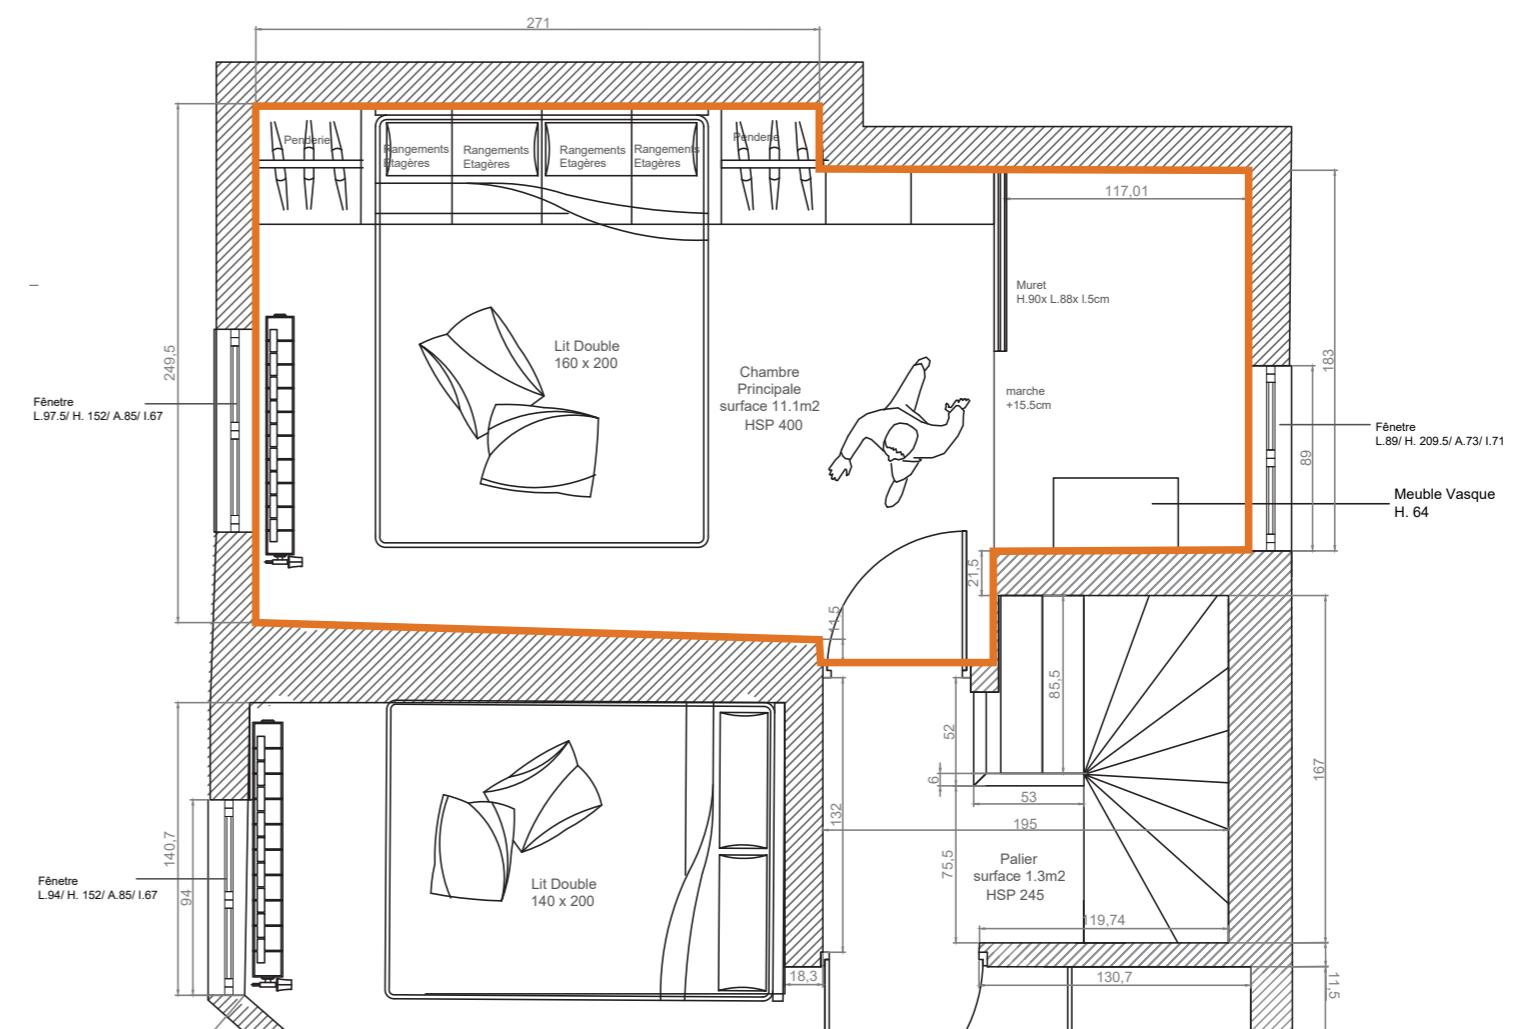


Renaissance

Réalisé au sein de l'agence d'Alexandra Barluet

Transformation du rez-de-chaussée d'un ancien relais de chasse, un lieu riche en charme et en histoire. L'objectif principal est de préserver son authenticité en mettant en valeur des éléments tels que l'escalier central, pièce maîtresse de l'espace. La rénovation combine confort moderne et respect de l'âme du lieu, créant un équilibre entre tradition et fonctionnalité.

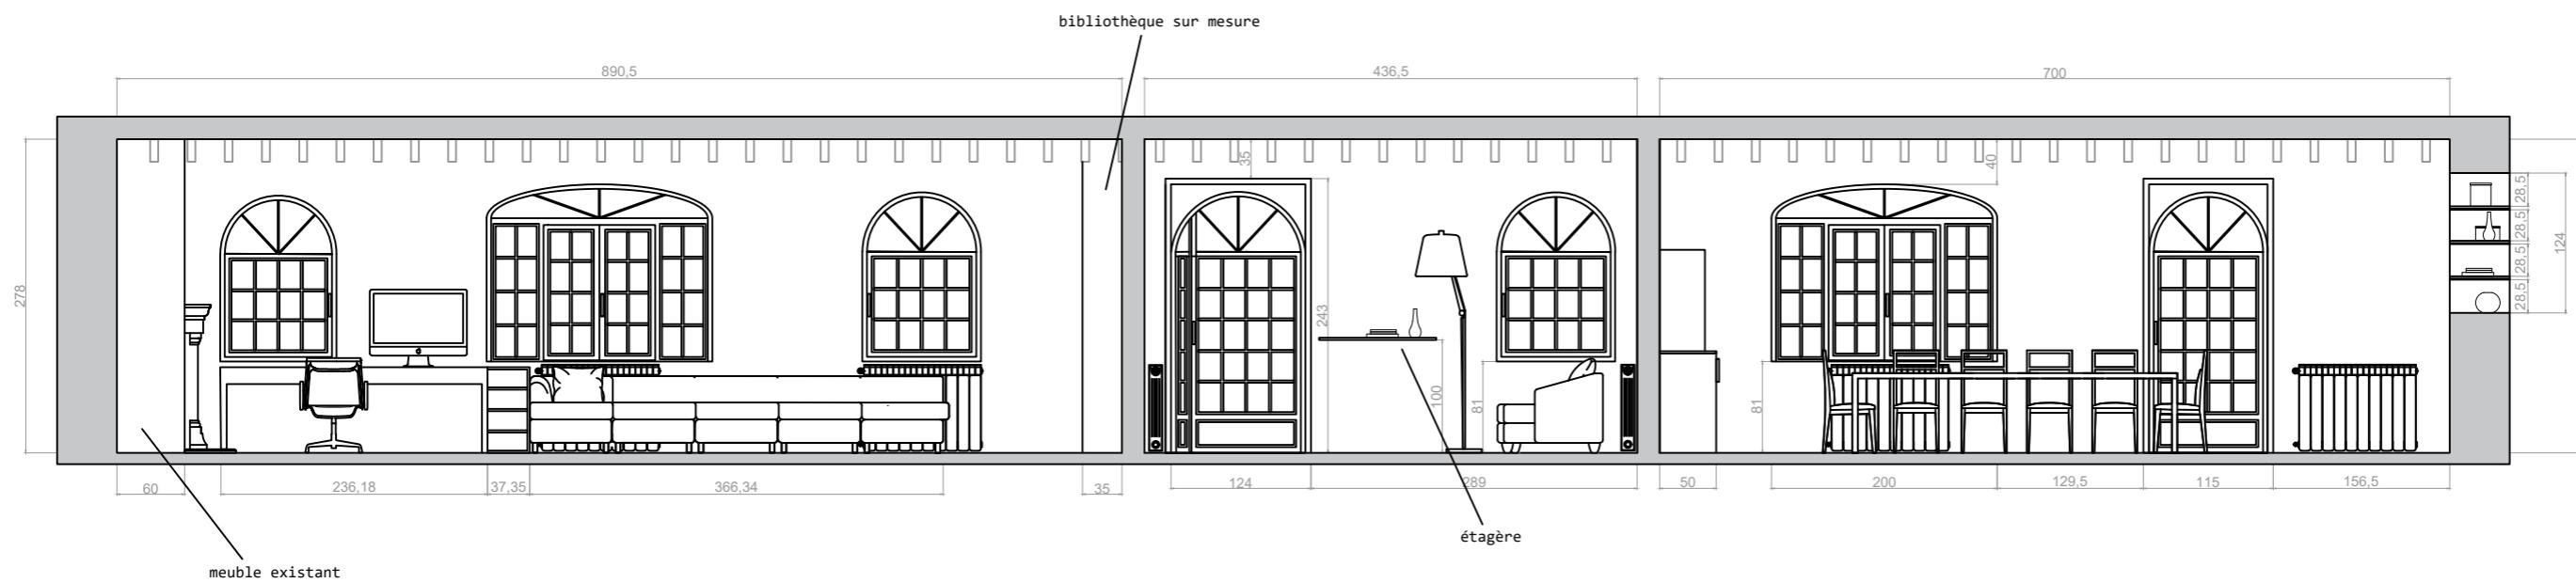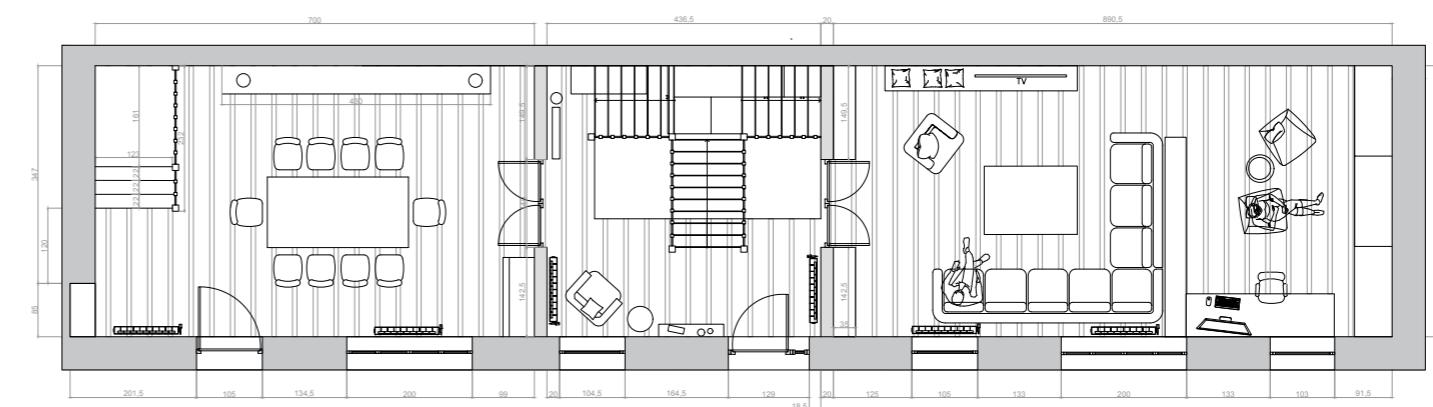

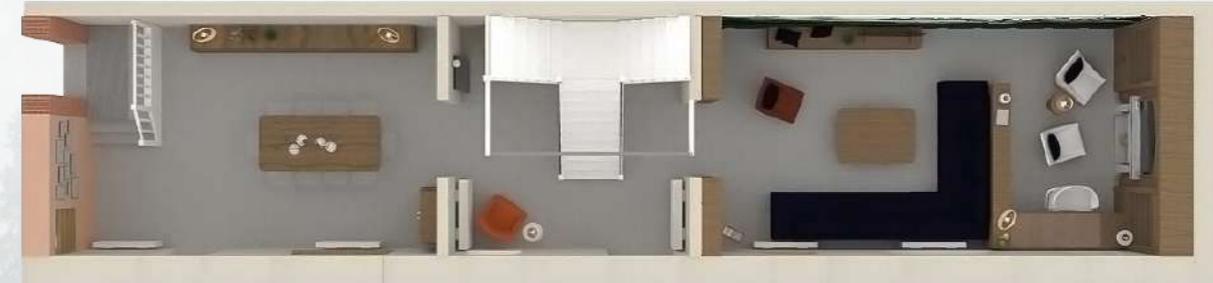

L'élément central du salon est la cheminée, accompagnée de ses deux bibliothèques murales intégrées, des pièces historiques méticuleusement préservées pour maintenir l'authenticité de l'espace. L'entrée a été soigneusement repensée afin de séparer clairement le salon de la salle à manger, optimisant ainsi la circulation tout en préservant l'intimité de chaque zone.


Des matériaux nobles et des couleurs chaudes ont été choisis pour renforcer l'atmosphère accueillante tout en apportant une touche contemporaine.





Réalisé au sein de l'agence d'Alexandra Barluet

Conception d'un meuble de salon sur mesure, alliant étagères horizontales et verticales créées spécifiquement pour l'espace, et intégration de caissons bas « Besta » d'Ikea pour répondre aux contraintes budgétaires. Cette approche permet de maximiser l'utilisation de l'espace tout en respectant un budget maîtrisé, sans compromis sur la fonctionnalité et l'esthétique.

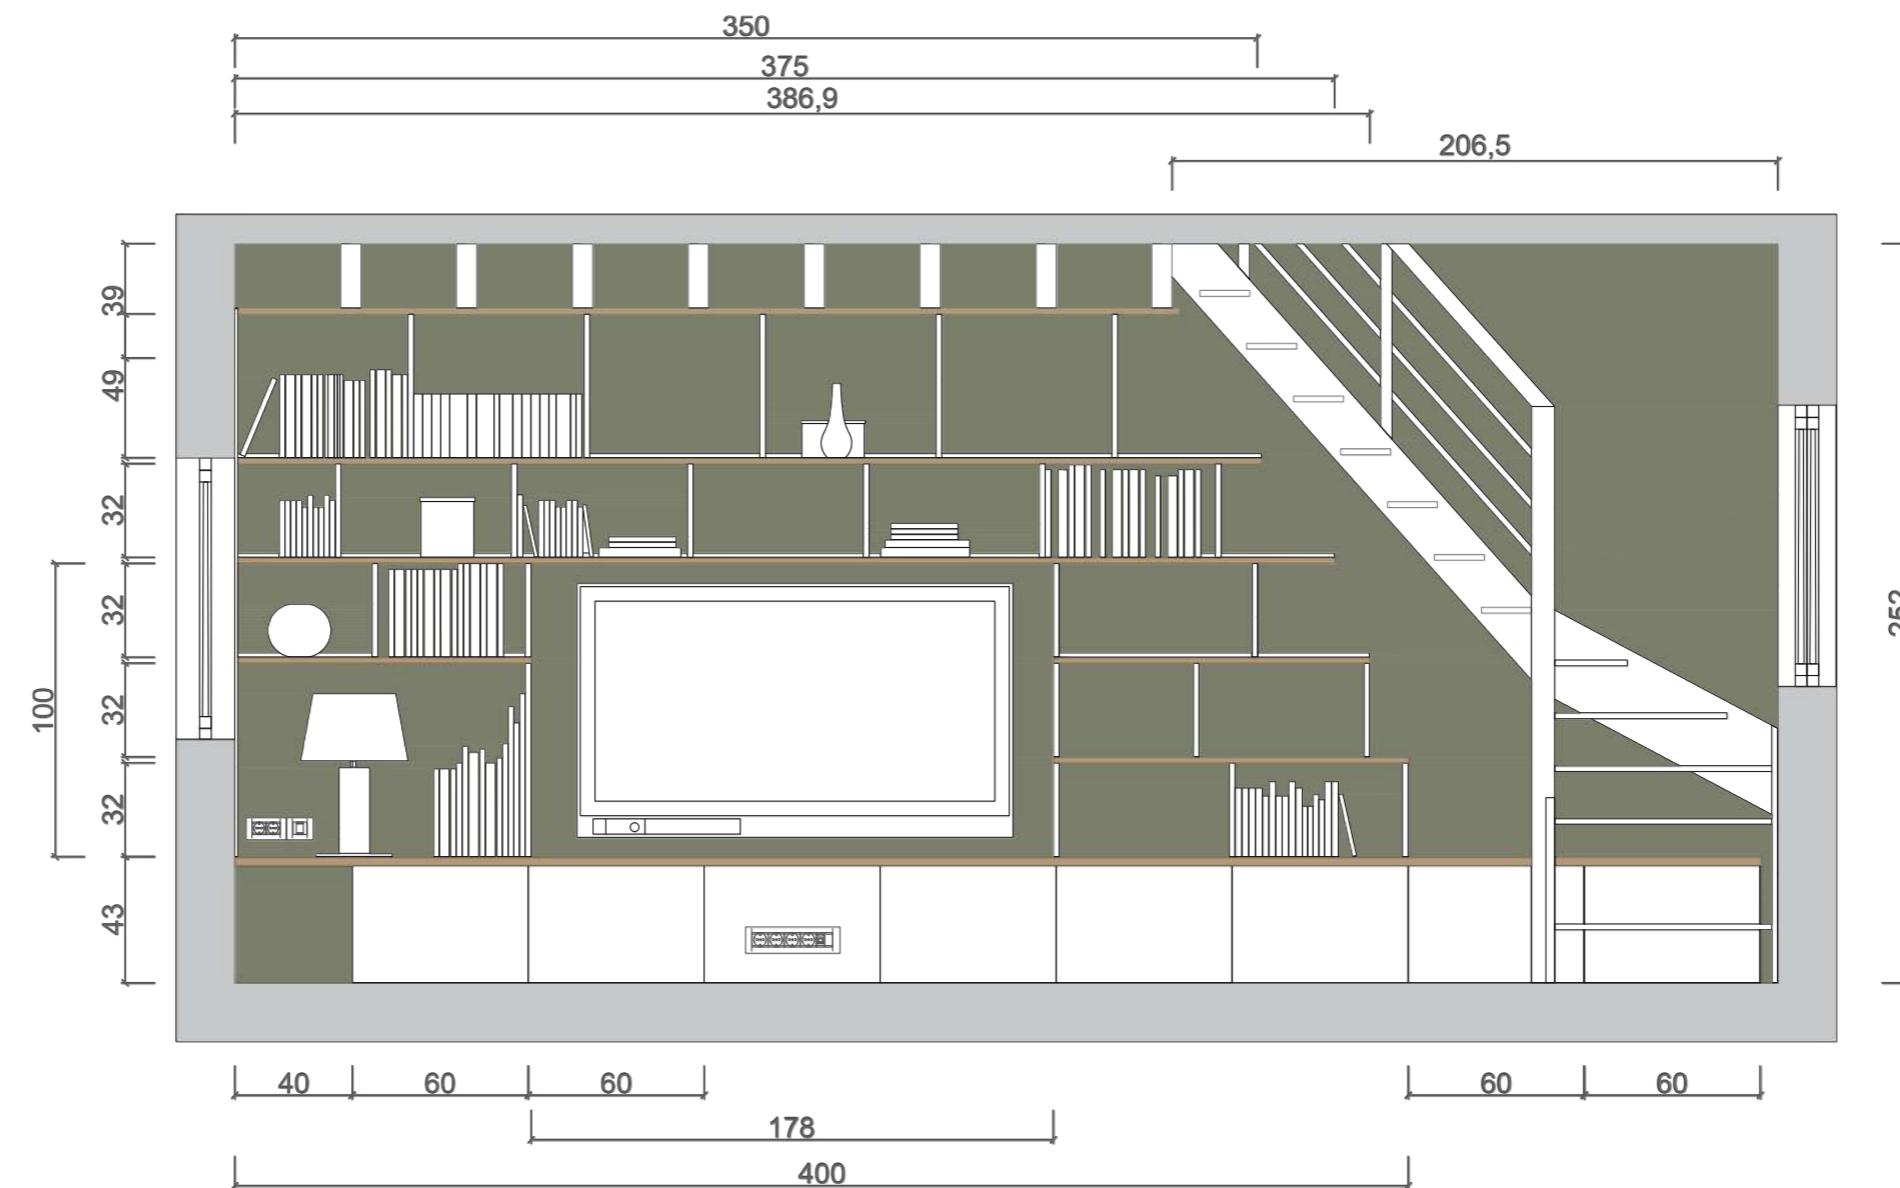





Des bandes LED discrètes sont intégrées sur toute la longueur des étagères, offrant un éclairage doux et chaleureux, parfait pour créer une atmosphère agréable le soir. Ces étagères sont conçues pour encadrer la télévision de manière subtile, l'intégrant harmonieusement dans l'ensemble du meuble sur mesure. Cette configuration permet de mettre en valeur l'équipement tout en conservant une esthétique épurée et fonctionnelle, en parfaite adéquation avec le design global du salon.



Studio 16

Réalisation de l'agence LNArch


Ce studio parisien, situé dans le 16^e arrondissement, a été repensé pour une mise en location adaptée à un jeune couple.

L'aménagement repose sur un principe de claustra et de mobilier amovible, permettant de moduler l'espace selon les besoins. Seules la salle d'eau et la cuisine restent fixes, les autres espaces sont modulables, permettant de s'adapter à différentes configurations.

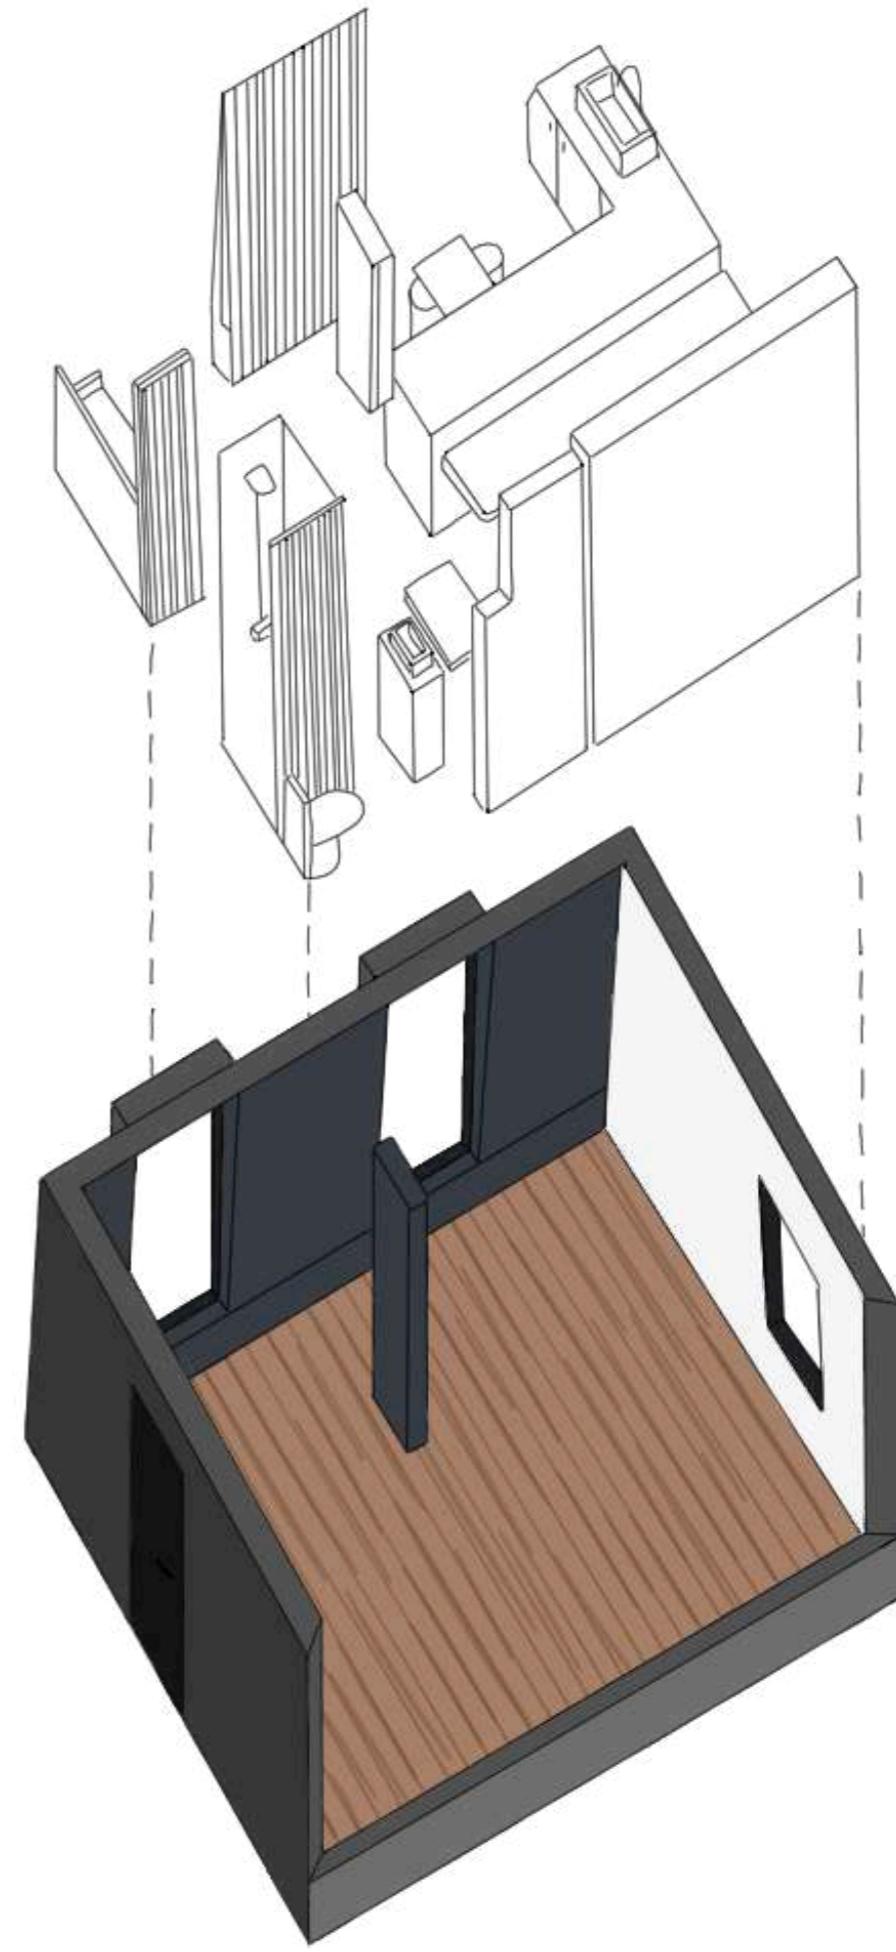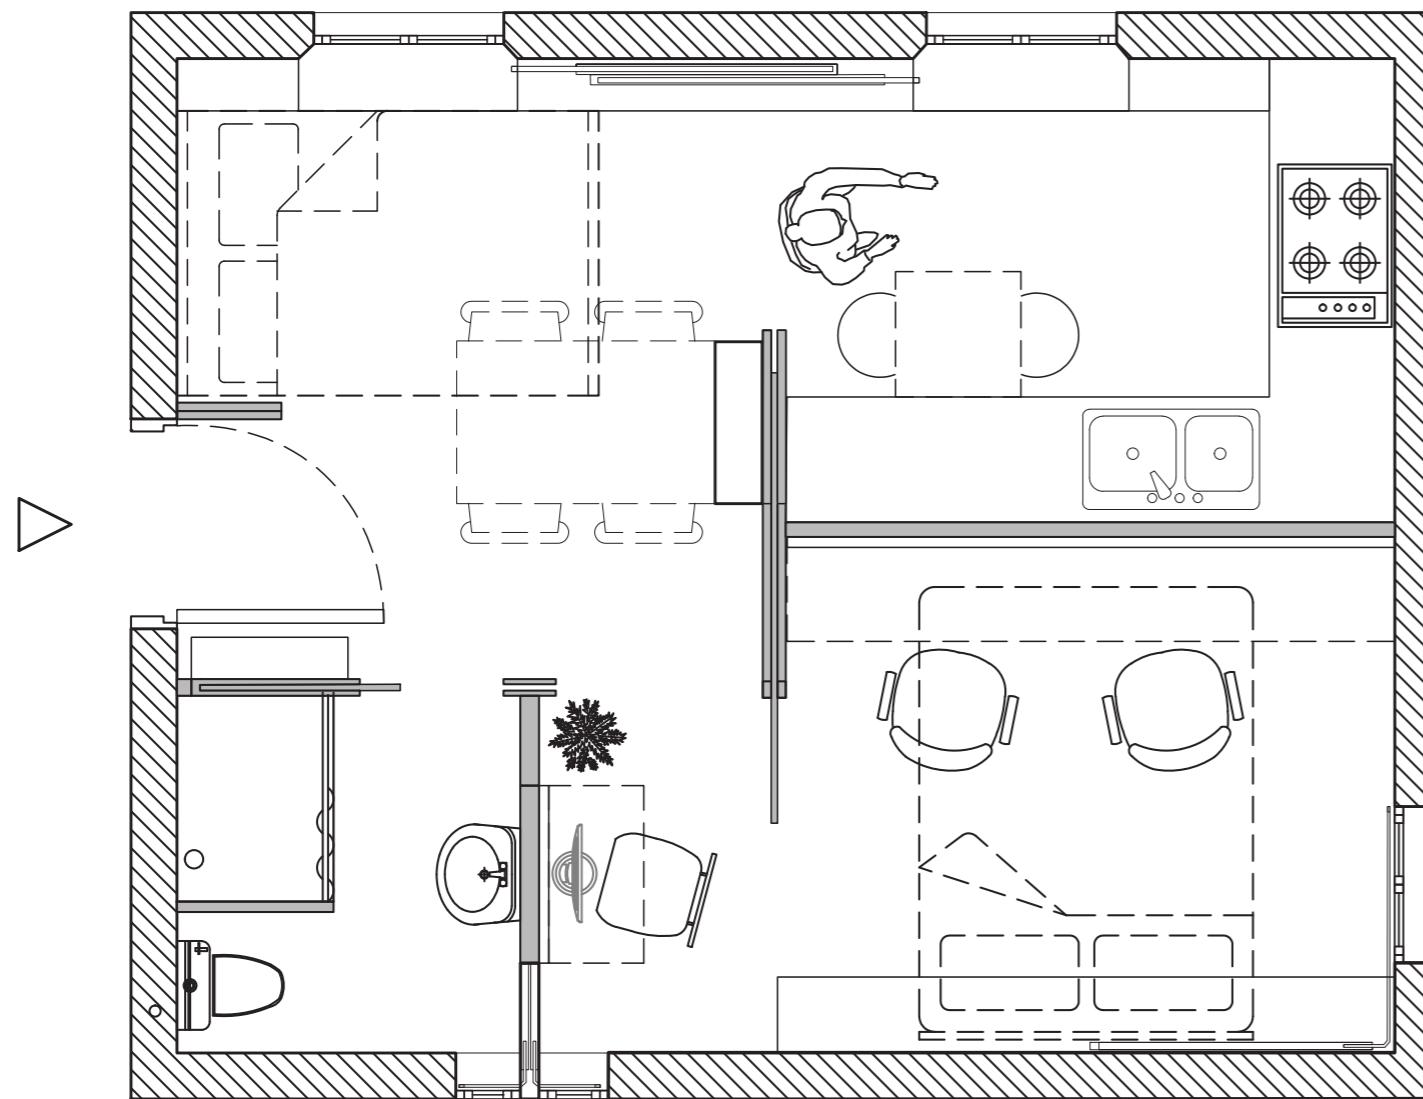


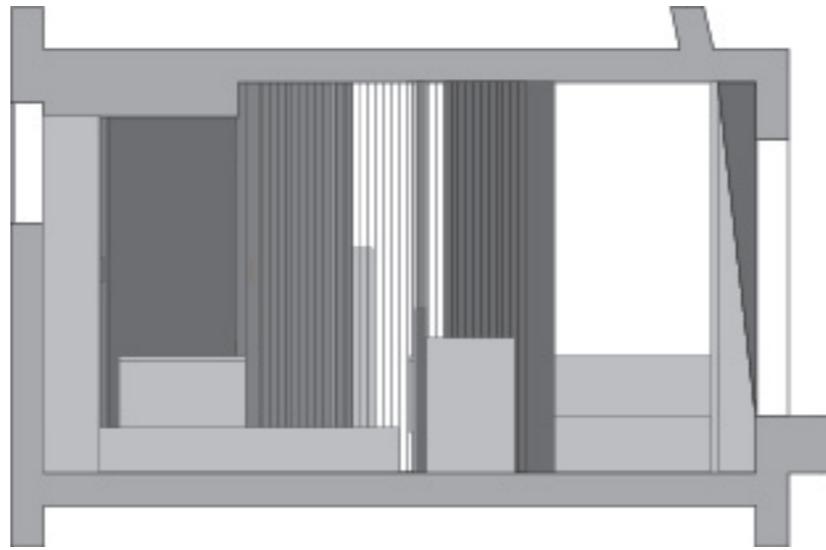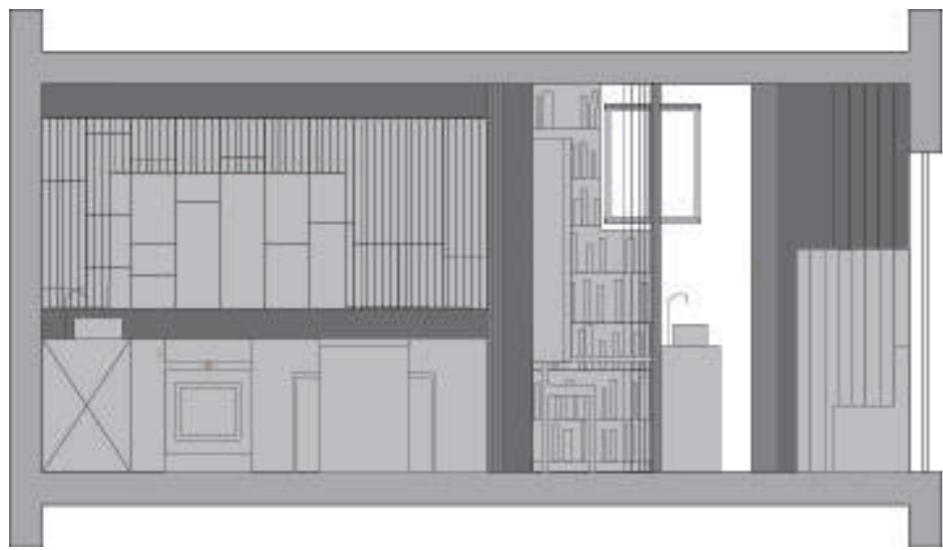

Présentation synthétique des coupes du projet pour accompagner le client dans ses choix de location avant la phase APS. Projet en cours.

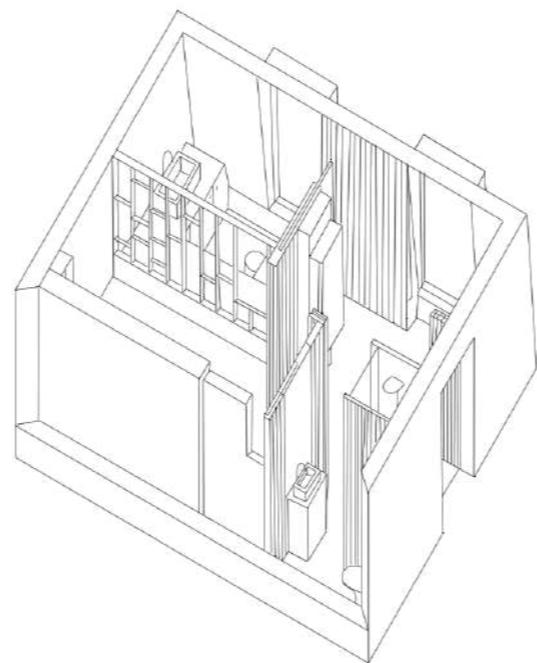


Le studio a été conçu pour offrir un maximum de polyvalence et de confort. Il permet d'accueillir deux invités supplémentaires pour la nuit, de partager un repas à quatre et de profiter de deux bureaux avec trois assises. Un dressing sur mesure, intégré à une niche avec lit escamotable, optimise le rangement. La cuisine circulaire, quant à elle, facilite la circulation.

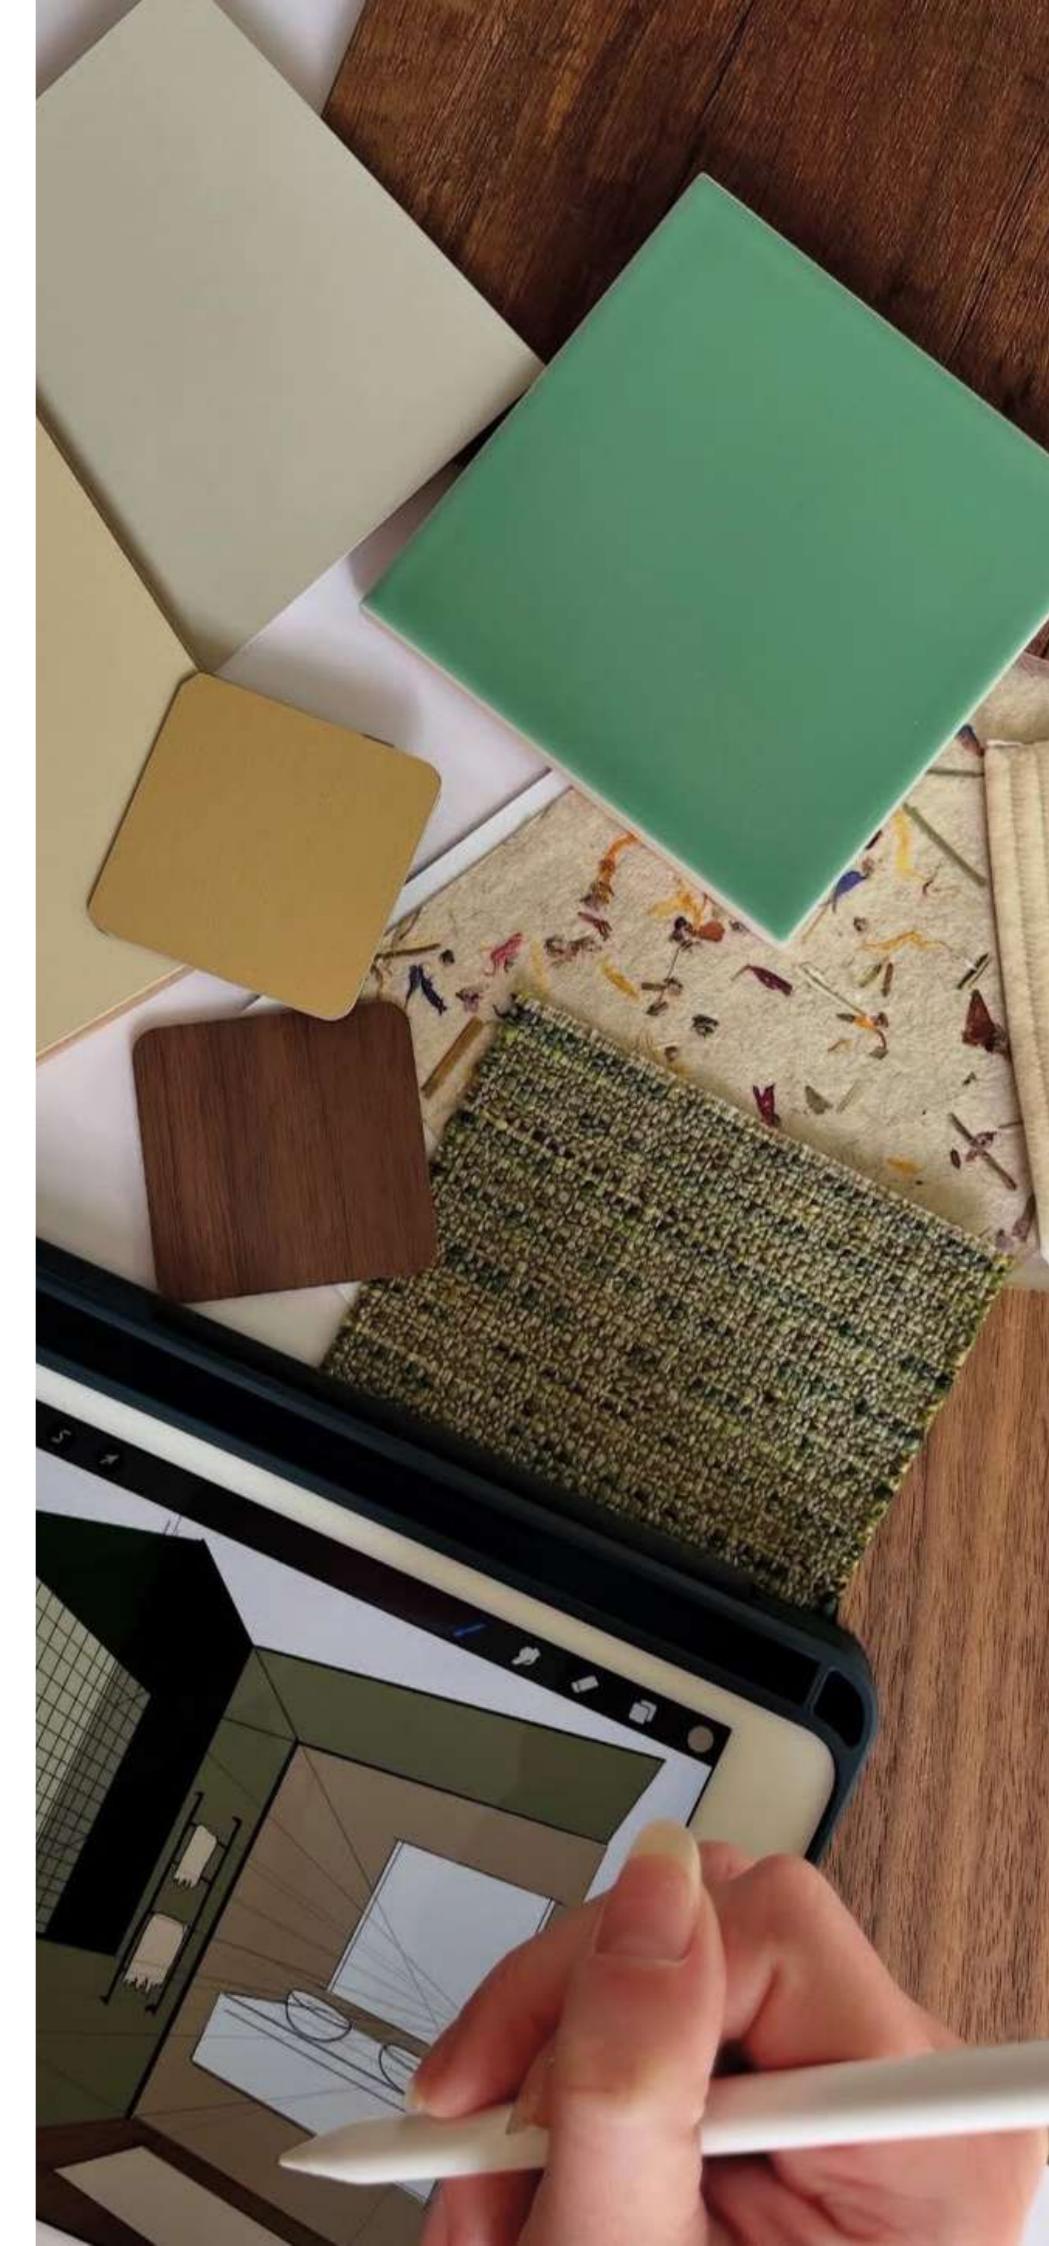

Au Fil des Marées

Réalisé au sein de l'agence d'Alice Frebourg

Conception et réalisation d'une bibliothèque sur mesure avec rangements bas, intégration de la télévision et du radiateur, ainsi que des niches ouvertes pour exposer les livres de manière esthétique. Le design tient compte des colombages de la maison normande et des poutres apparentes au plafond.

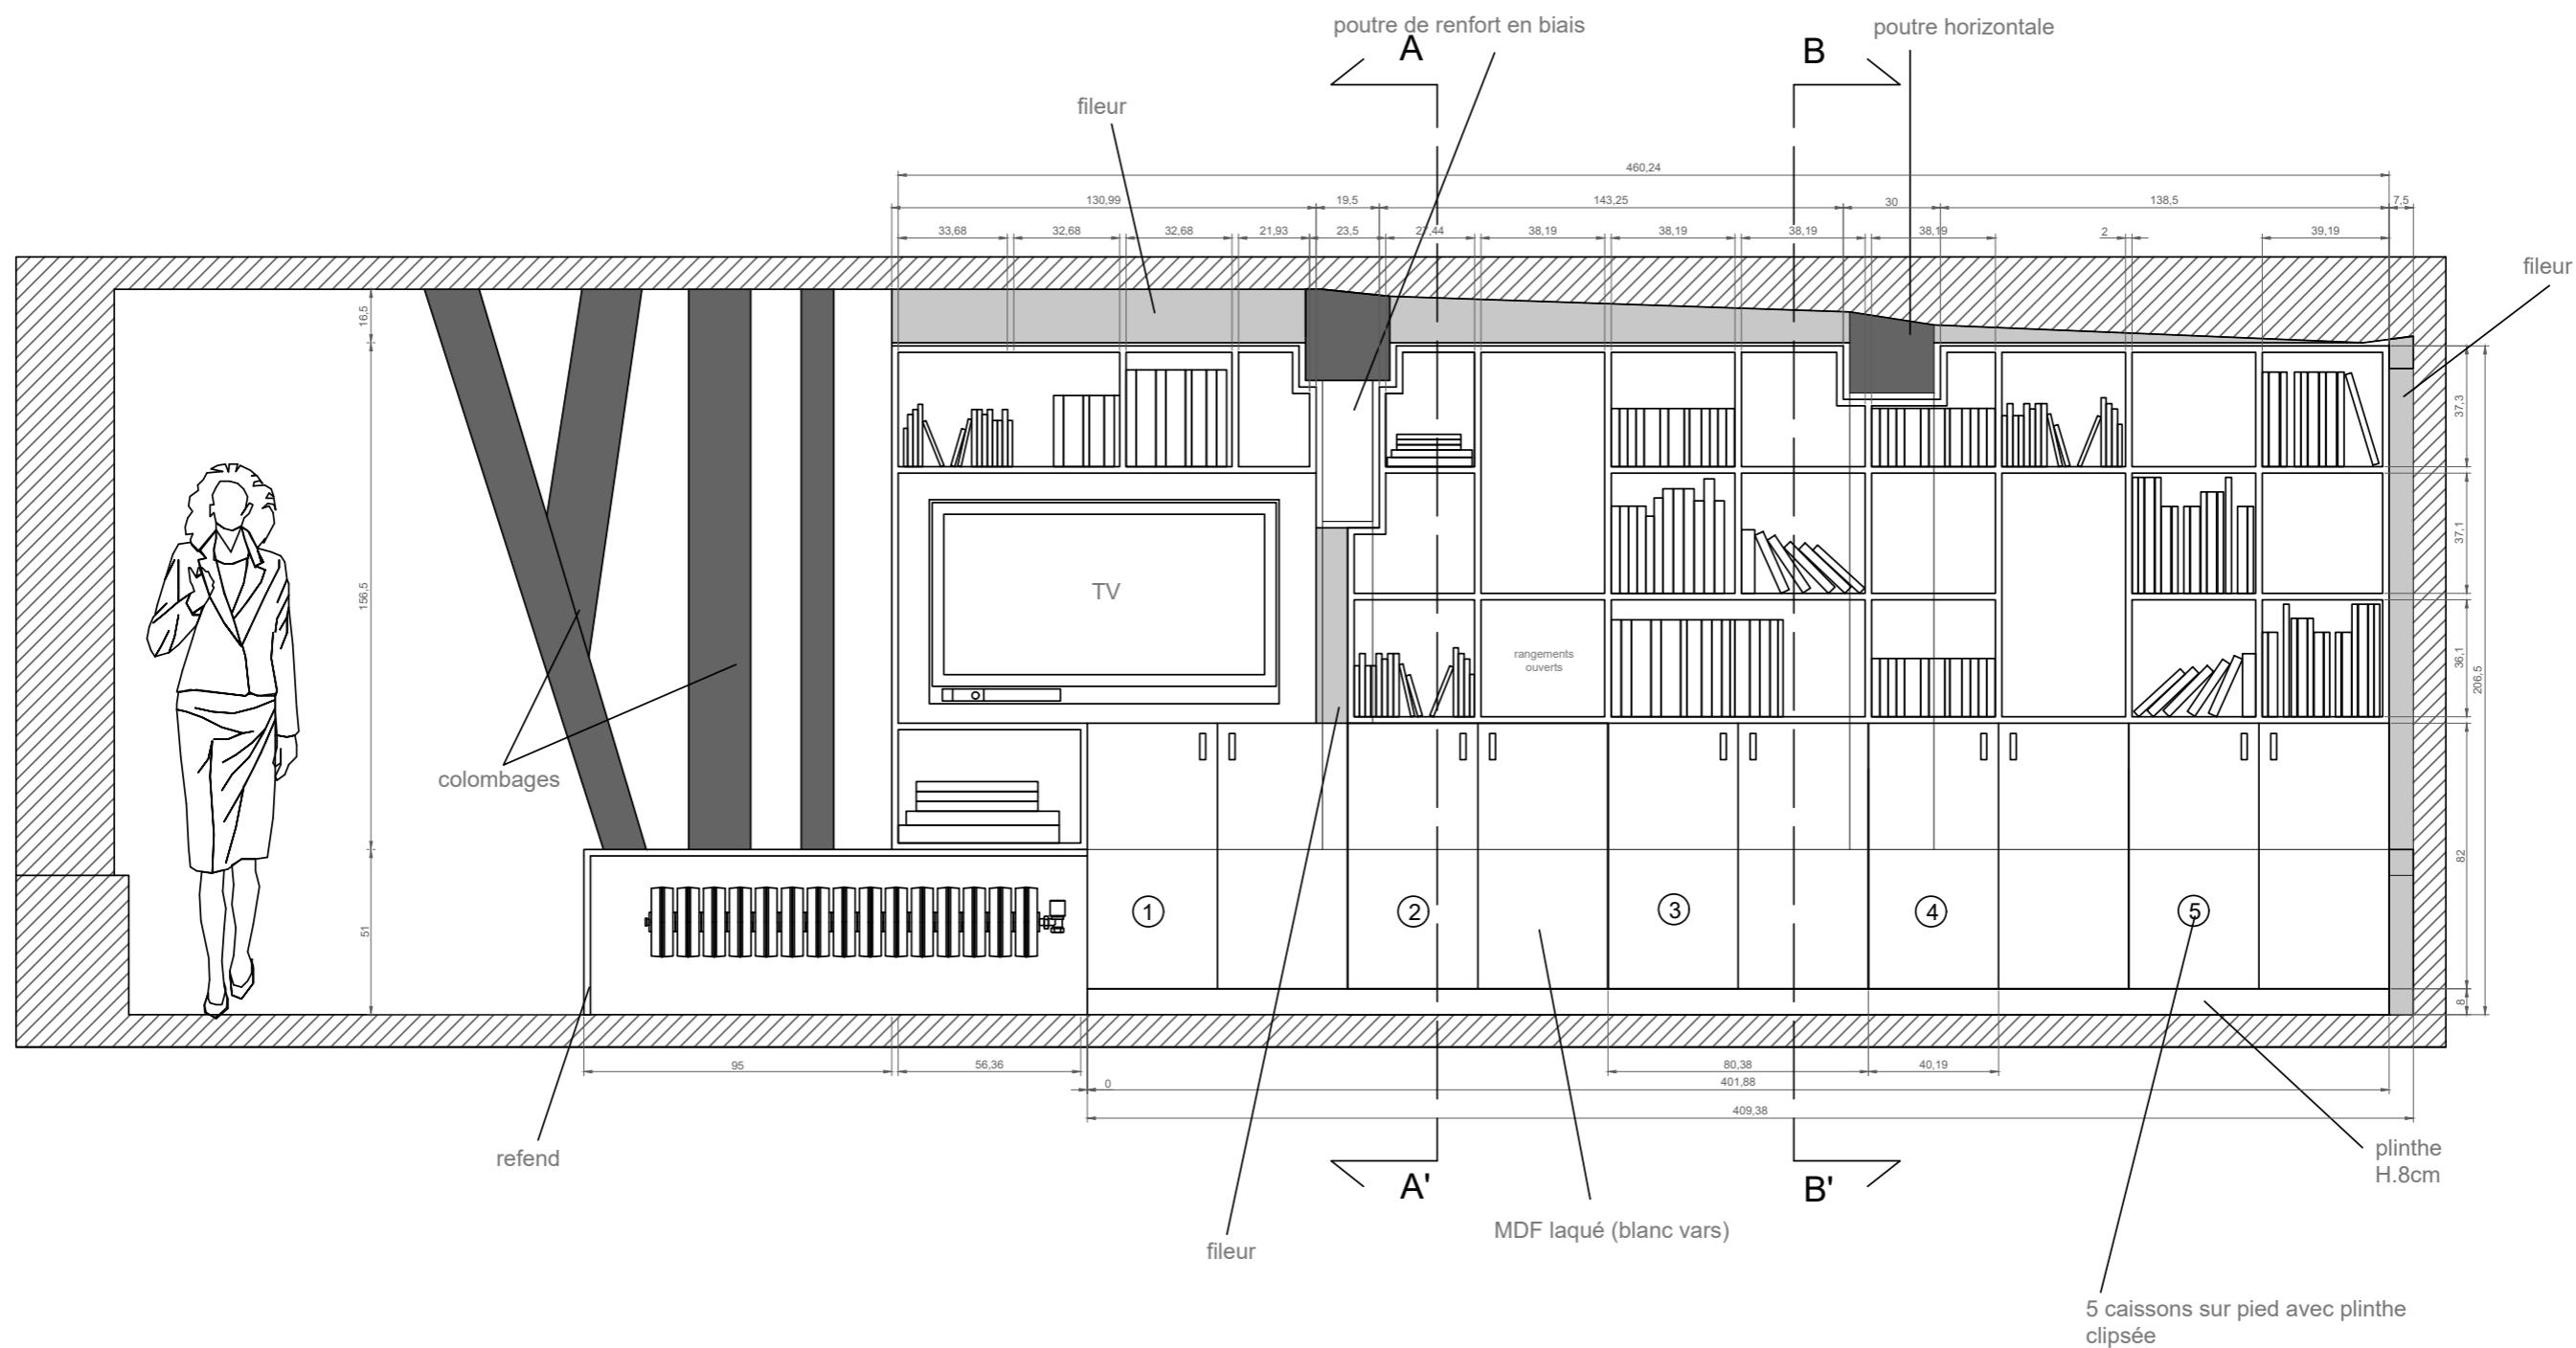








Pour permettre à la chaleur du radiateur de circuler sans altérer la tablette supérieure, des percements ont été créés. Cela optimise l'utilisation du radiateur tout en prolongeant esthétiquement la bibliothèque dans le salon.

Signature

Réalisation de l'agence LNArch

Biblio'Trio est une gamme de mobilier polyvalente, offrant trois fonctions distinctes. Composée de formes organiques, elle comprend une banquette 2 places, une lampe sur pied avec éclairage LED, et un meuble de rangement, le tout formant une bibliothèque fonctionnelle et esthétique.

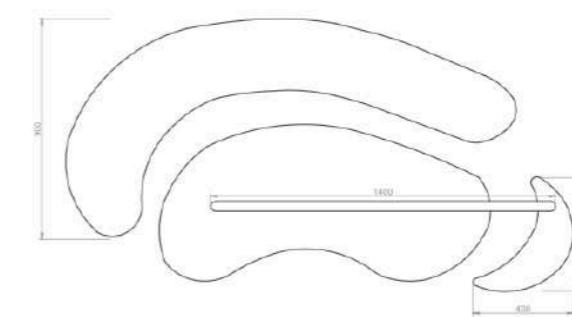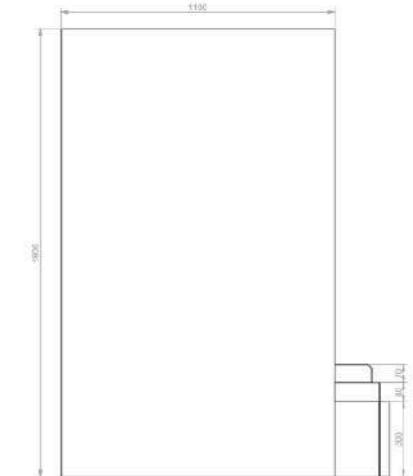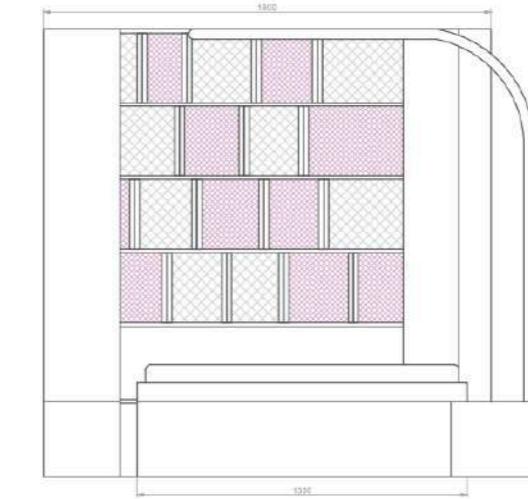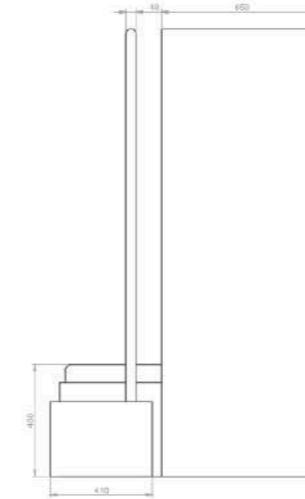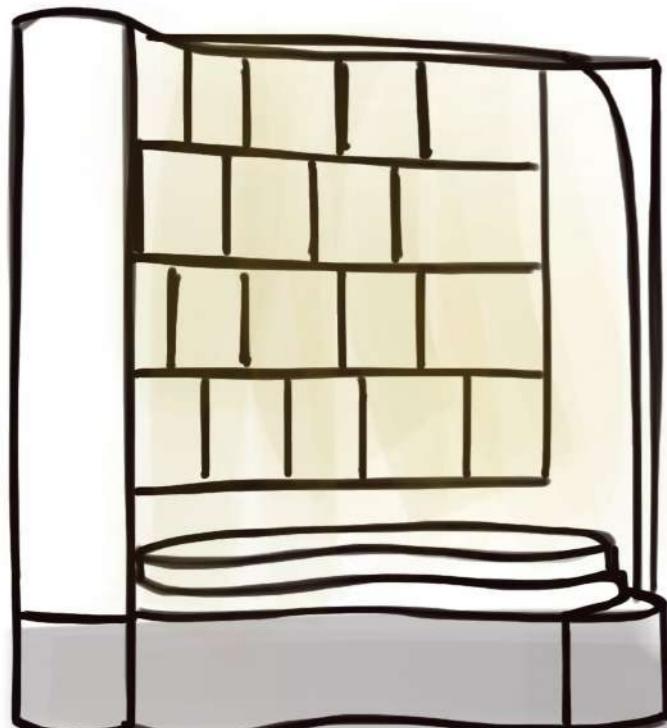




Les pièces de la gamme Biblio'Trio sont fabriquées en ABS teinté mat, un matériau reconnu pour sa résistance et sa légèreté, garantissant ainsi une durabilité sans compromettre la maniabilité.

Chaque élément est ensuite recouvert de laiton, créant un motif continu et élégant qui unifie l'ensemble tout en apportant une touche sophistiquée. L'assise de la banquette et le fond du meuble de rangement sont habillés de velours, offrant une texture douce et agréable au toucher, contrastant subtilement avec la rigueur des autres matériaux.

Cette alliance de matériaux soigneusement choisis offre un équilibre parfait entre design raffiné et praticité optimale.

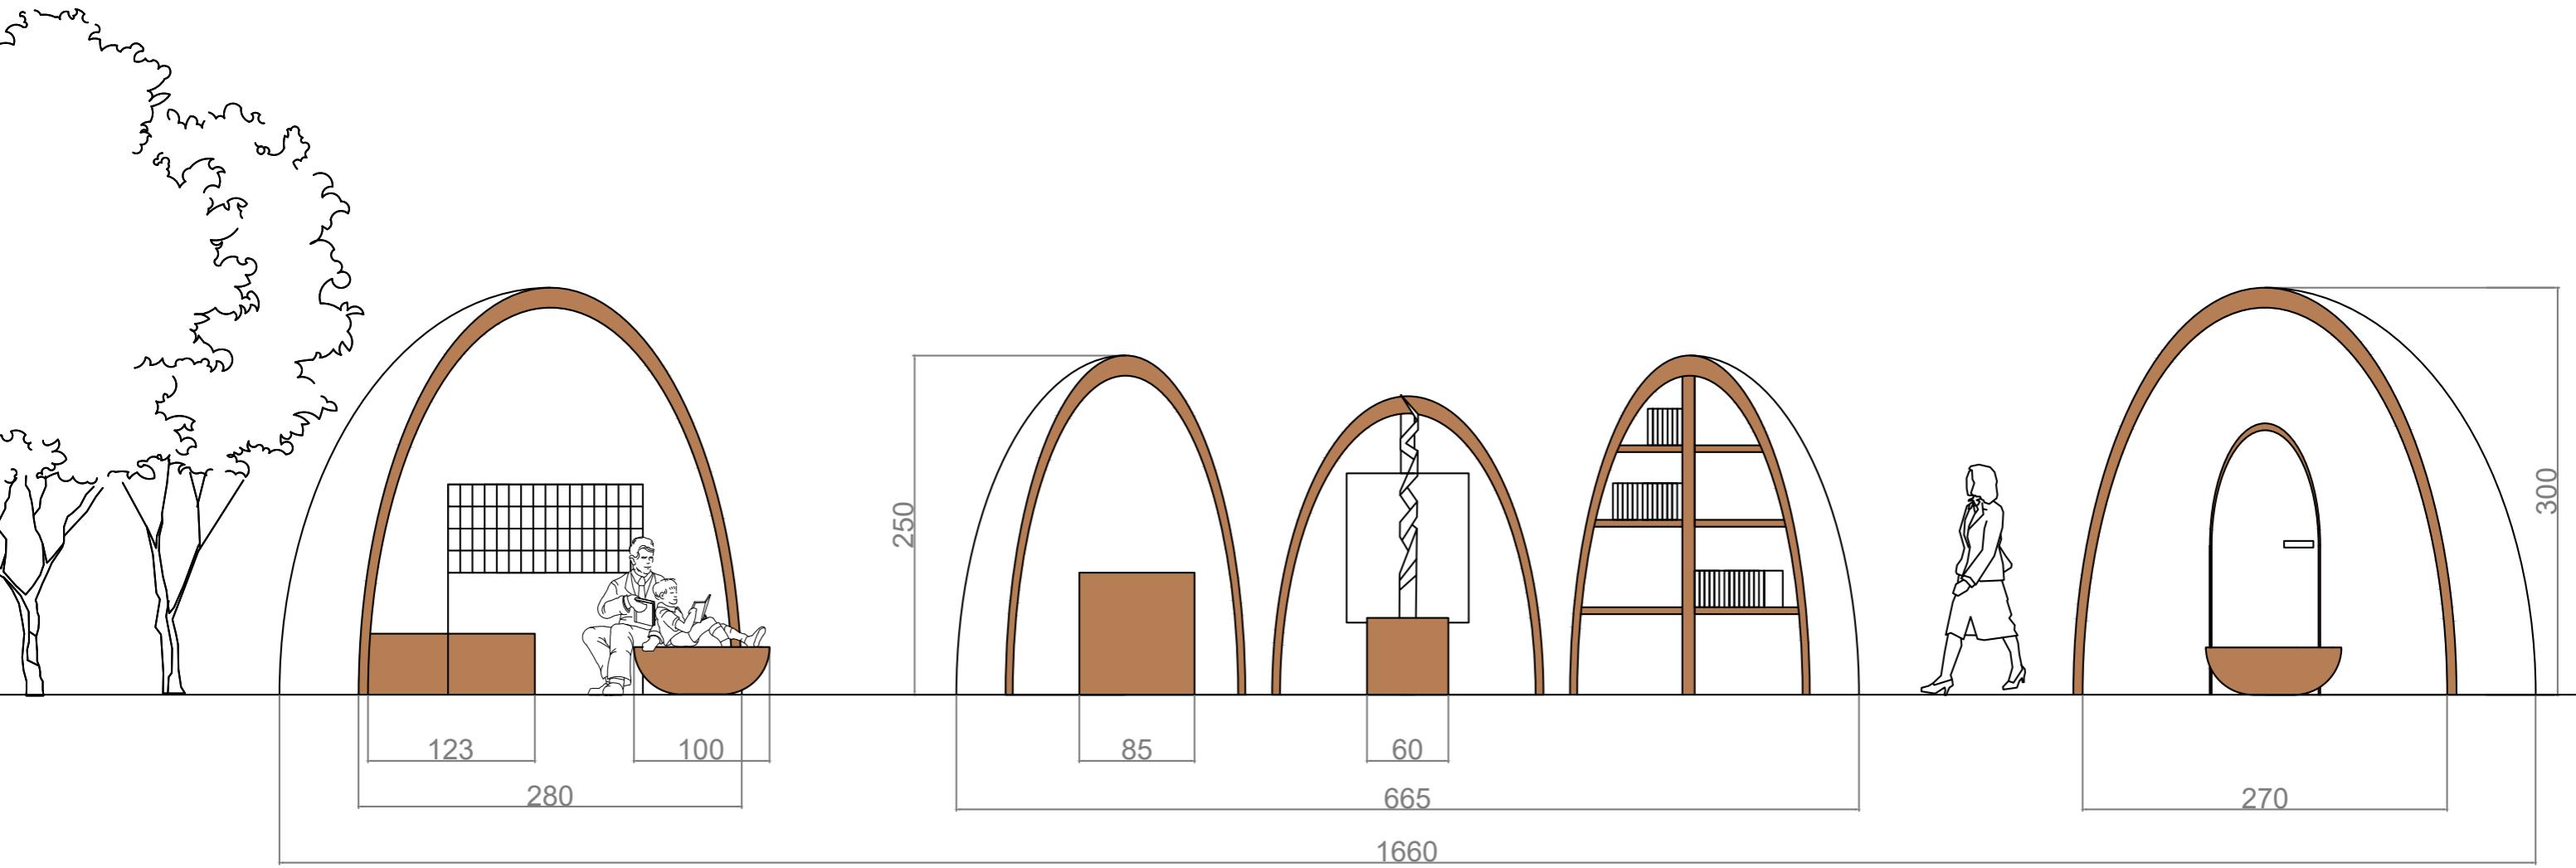

SOMMAIRE PROJETS CLIENTS PROFESSIONNELS

01. Cohésion

Aménagement de 5 loges d'accueil pour un bailleur social.

02. L'Atelier

Création du concept d'un restaurant gastronomique.

03. Drakkar

Suivi de chantier d'un musée immersif sur l'univers des Vikings.

04. Rhizome

Conception d'une péniche itinérante le long du fleuve du Rhône.


05. Gourmandise

Réalisation du DCE d'un restaurant/ sandwicherie de 400m².

Gohésion

Réalisé au sein de l'agence Atelier Madame

Conception du nouveau concept et aménagement de cinq loges d'accueil pour un bailleur social en banlieue parisienne, visant à rafraîchir ces espaces et optimiser leur fonctionnalité pour offrir un environnement agréable et pratique.

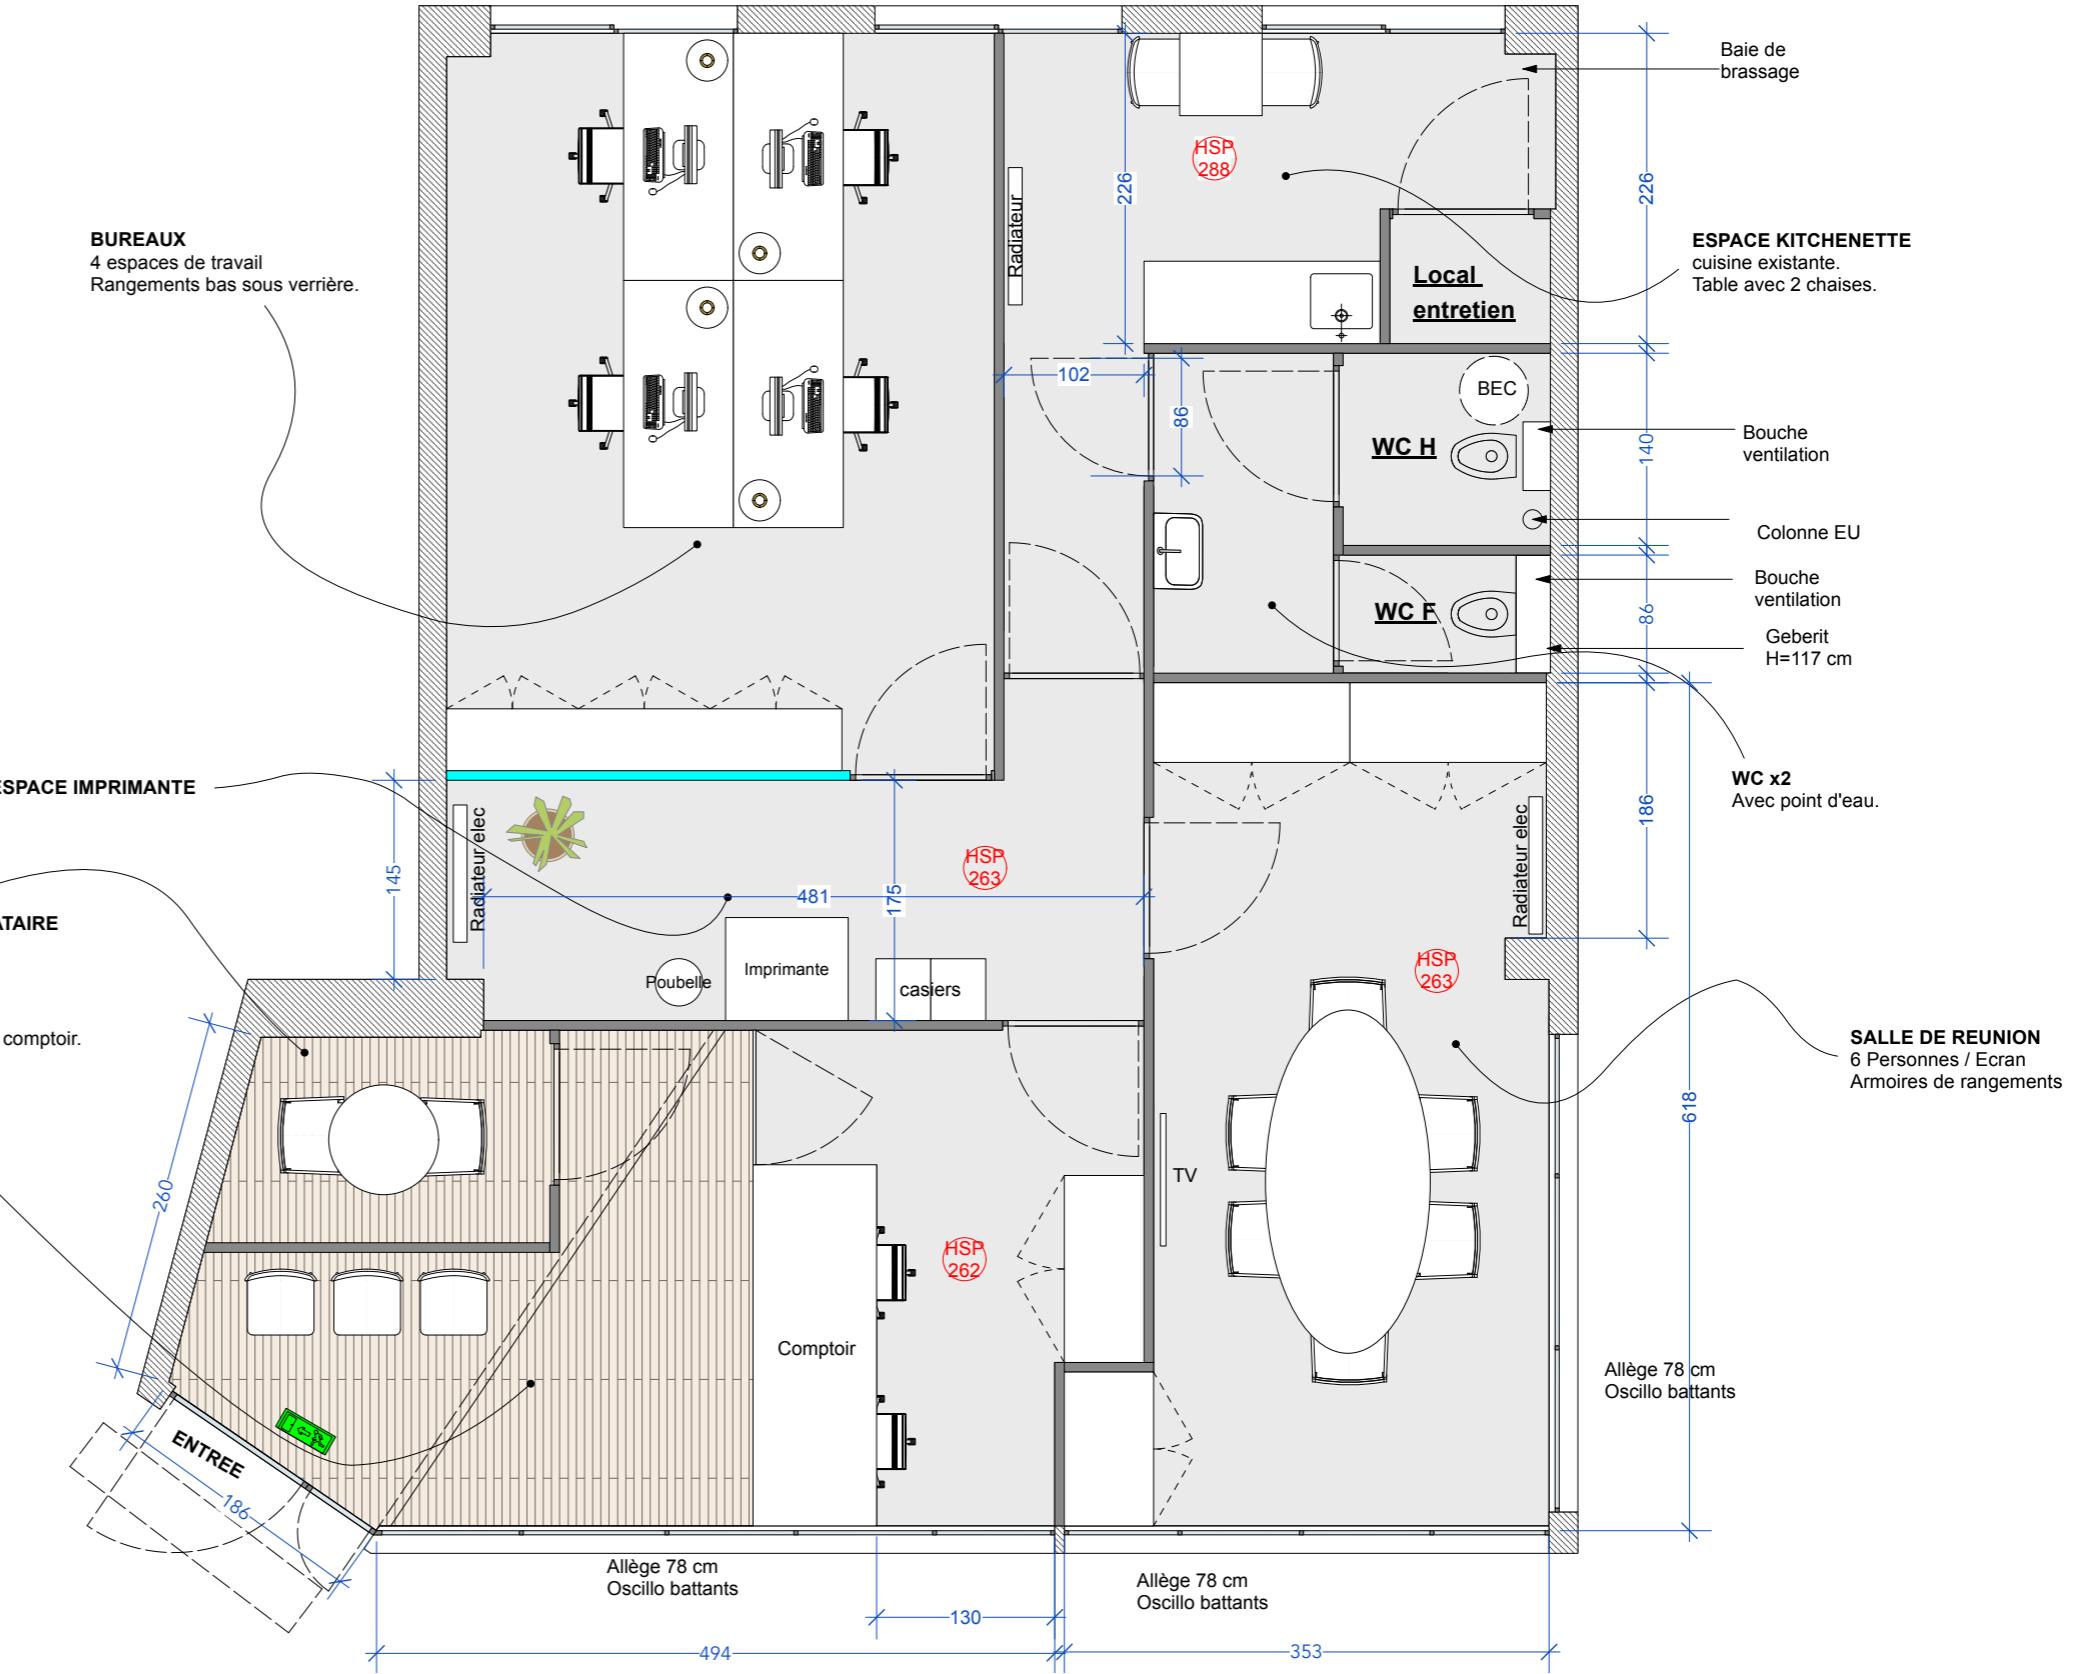




Bureau droit SIERRA
Gosto.com



Suspension LED René
Las Sola



Plafonnier ORBIT IV - blanc
Luminaire.fr

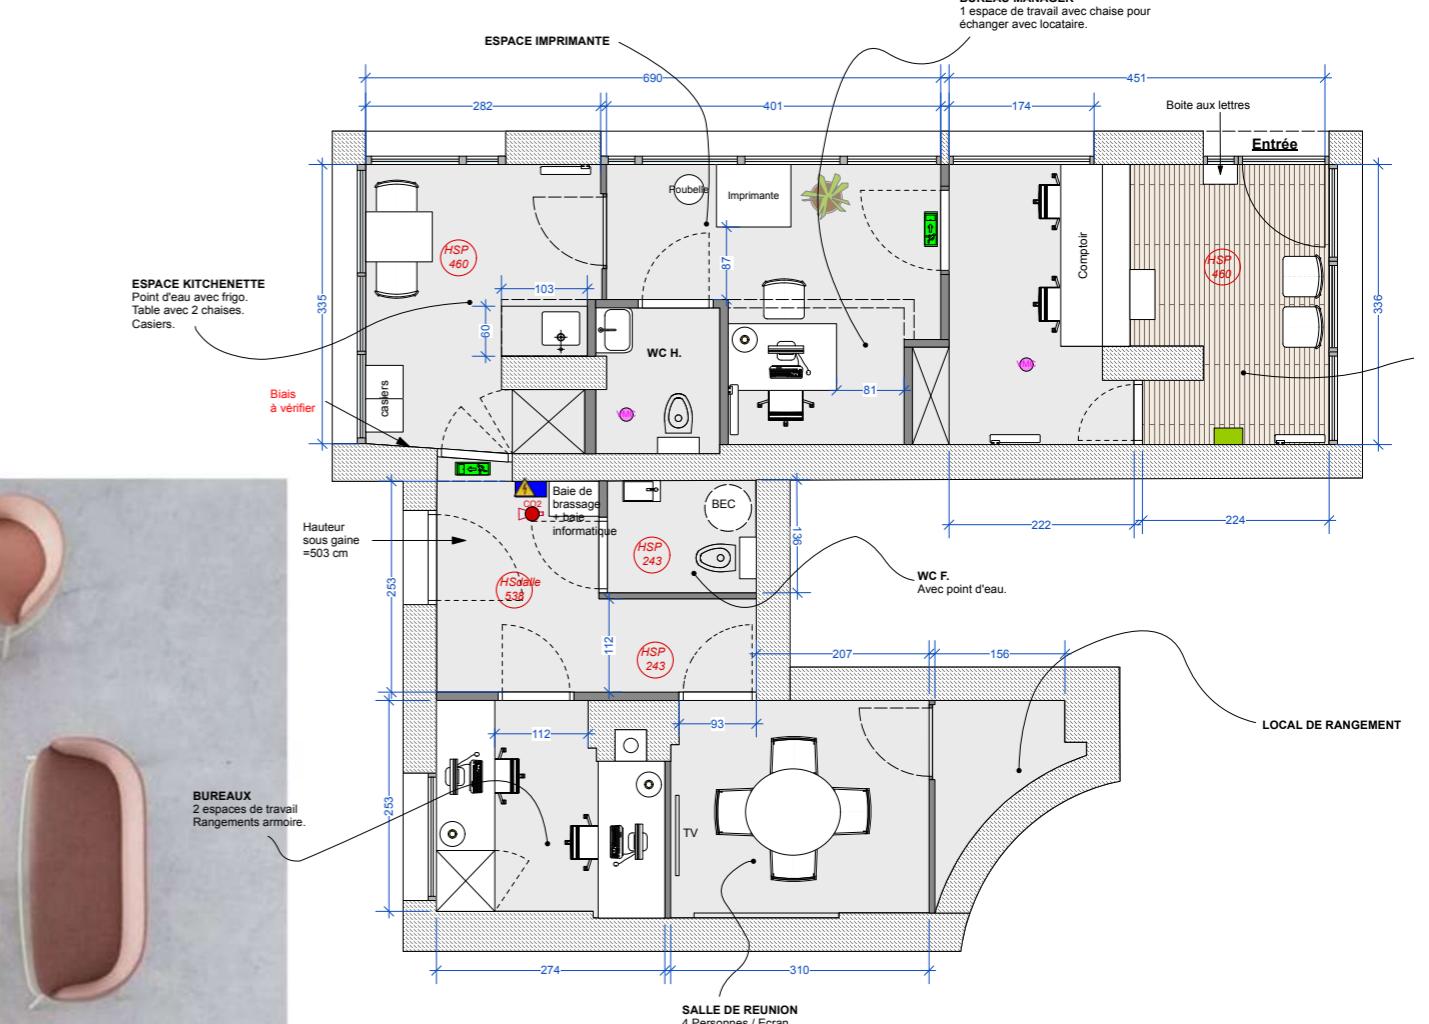



L'objectif est d'améliorer l'accueil en tenant compte des contraintes techniques et des besoins spécifiques de chacun. Le projet propose des solutions modernes et fonctionnelles, favorisant la fluidité des échanges et le confort.

Chaque loge est conçue autour d'une couleur dominante issue du logo du bailleur, apportant à la fois de la couleur et une personnalisation unique à chaque espace, tout en maintenant une atmosphère professionnelle et accueillante.


L'Atelier


Réalisation de l'agence LNArchitecte

« Dans les étoiles » est un restaurant gastronomique, conçu autour du concept d'atelier-bar, où la cuisine est entièrement visible par les convives. Il propose un spectacle de ciel étoilé, aussi bien en journée qu'en soirée, avec une luminosité adaptée à chaque moment de la journée.

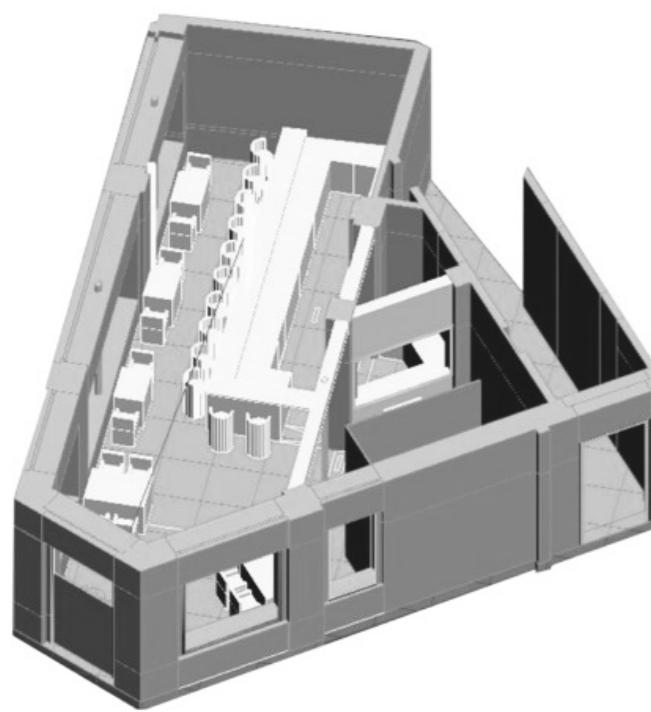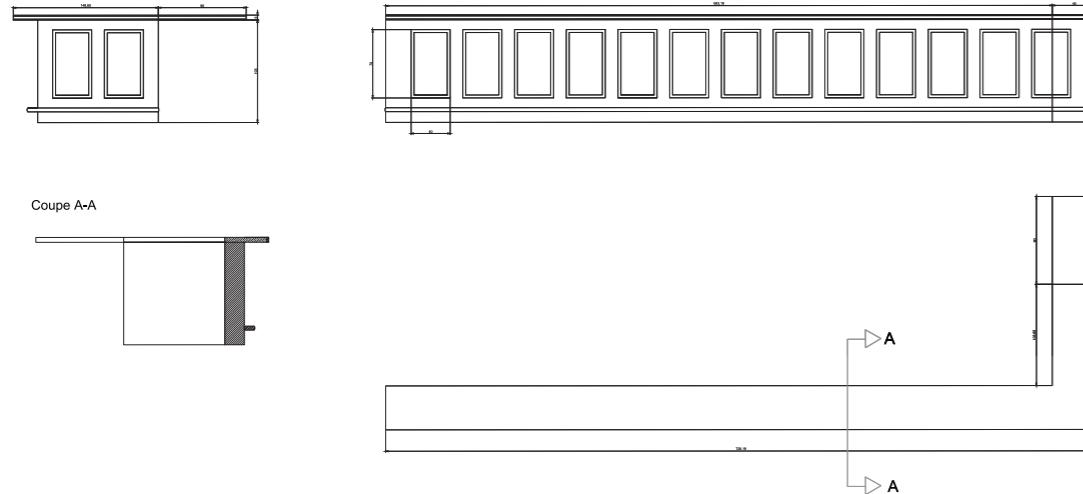


Vue globale - 3D rendu simplifié

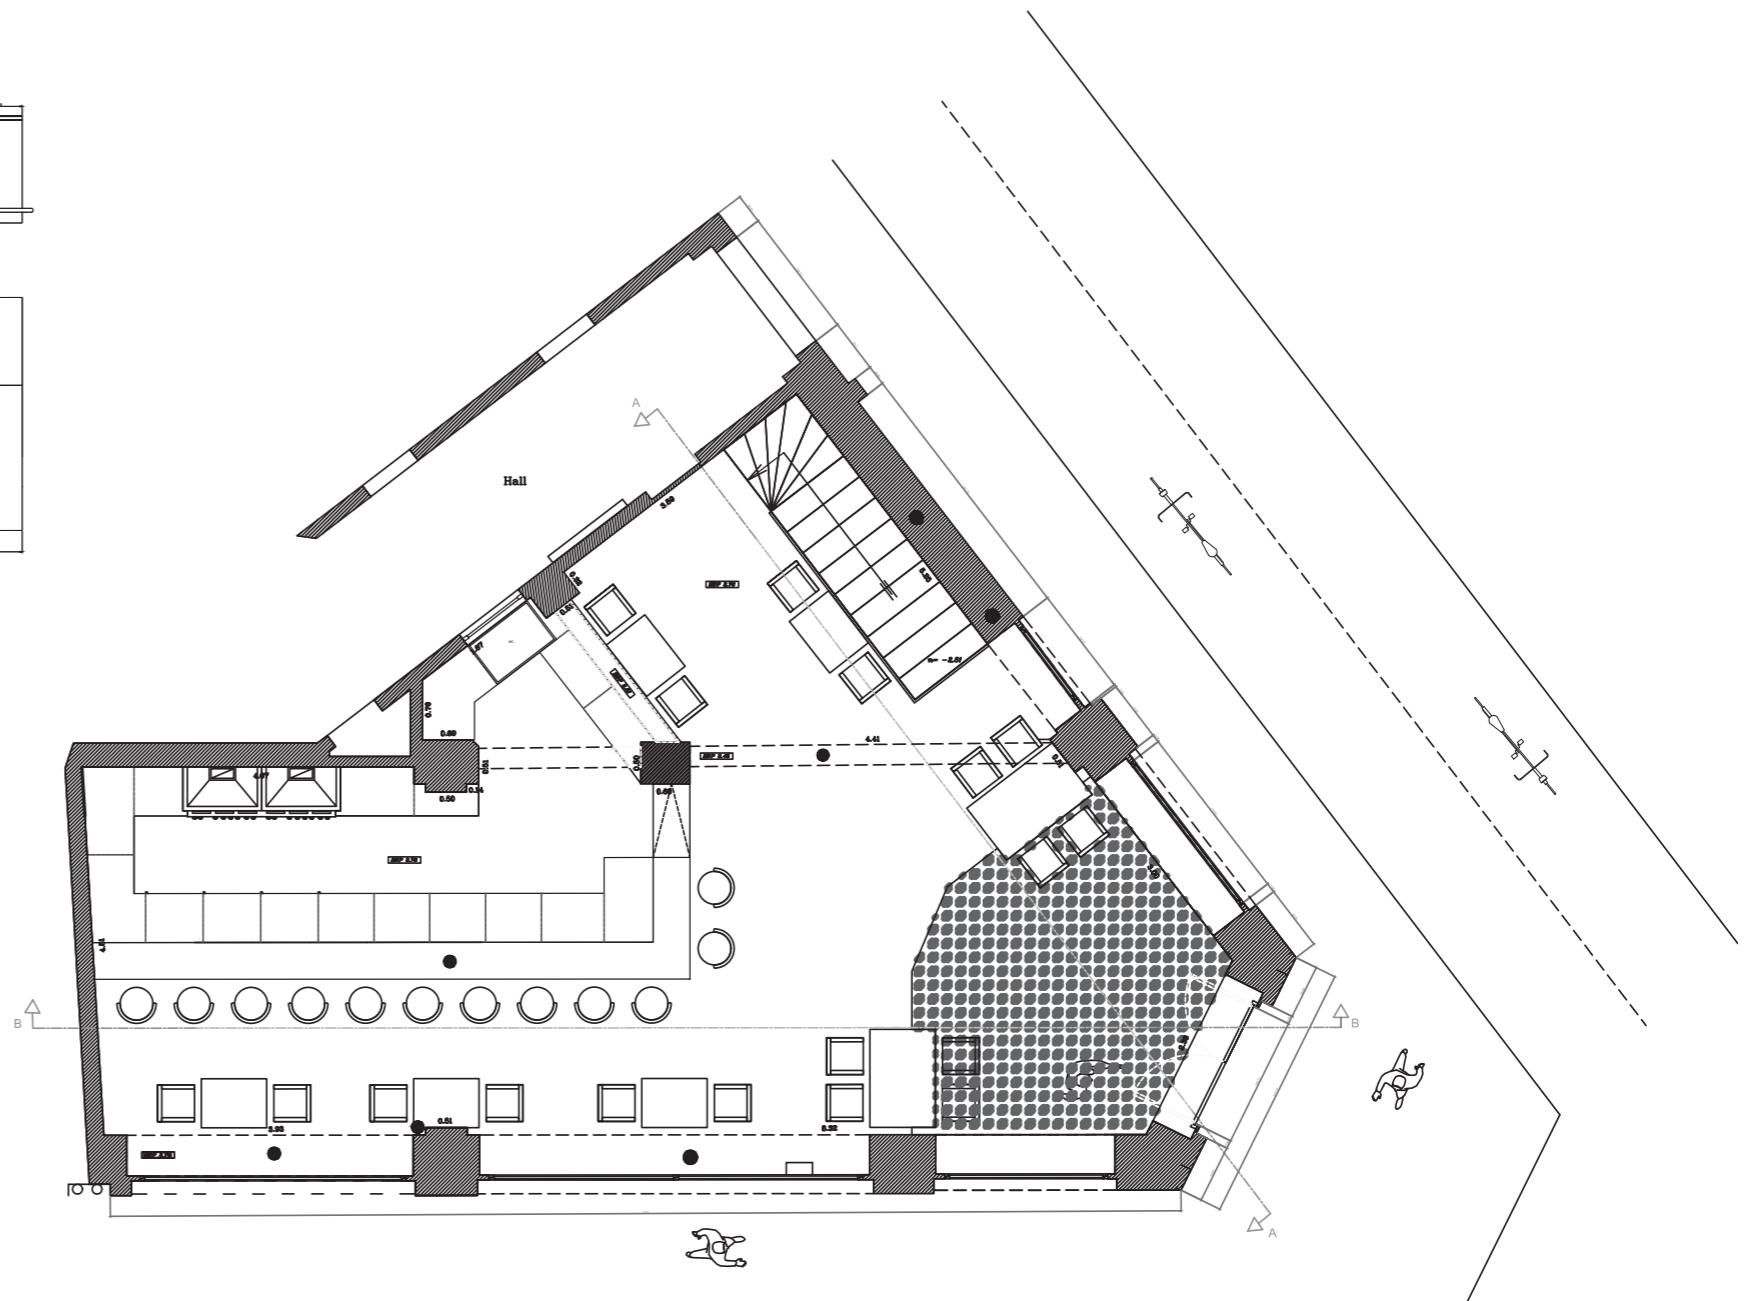

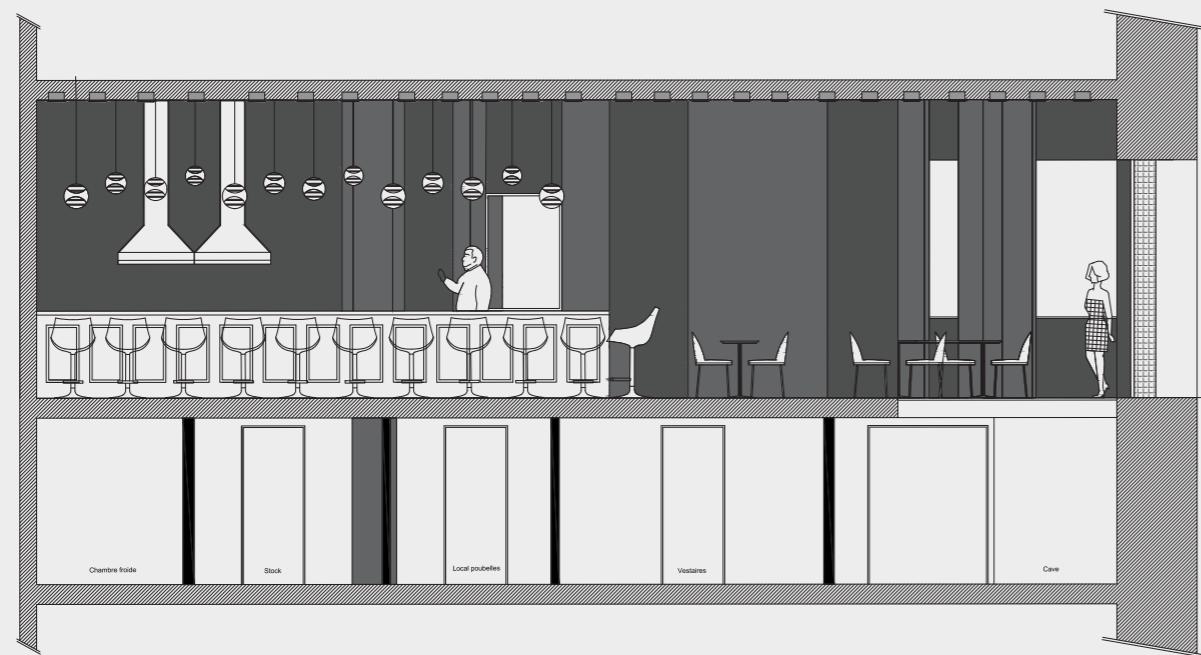

Situé dans le 3ème arrondissement de Paris, le restaurant s'inspire de l'Atelier de Joël Robuchon, en apportant une touche de chic et d'intimité grâce à l'association de velours, marbre noir, bois et laiton. La devanture sobre, composée de vitres teintées, ne laisse pas deviner le concept du lieu depuis l'extérieur. C'est en pénétrant par curiosité à l'intérieur que l'on plonge véritablement dans son univers raffiné.

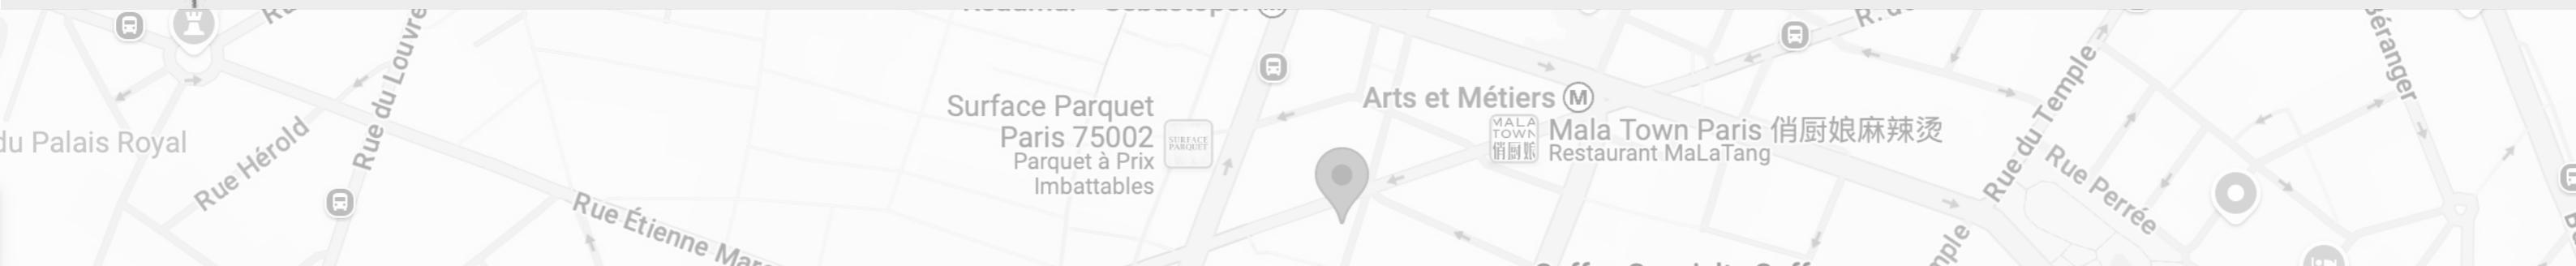


Drakkar

Réalisé au sein de l'agence Atelier Madame

Réalisation du dossier d'aménagement pour l'administration française en vue du lancement des travaux et du suivi de chantier d'un musée immersif sur l'univers des Vikings au centre commercial Carré Sénart à Lieusaint. Le projet inclut l'agencement des espaces, l'intégration de technologies interactives et immersives, et des solutions acoustiques et visuelles. En tant que cheffe de projet maître d'œuvre, j'ai assuré le respect des délais, des normes de sécurité et la coordination entre les intervenants.



Elévation façade simplifiée

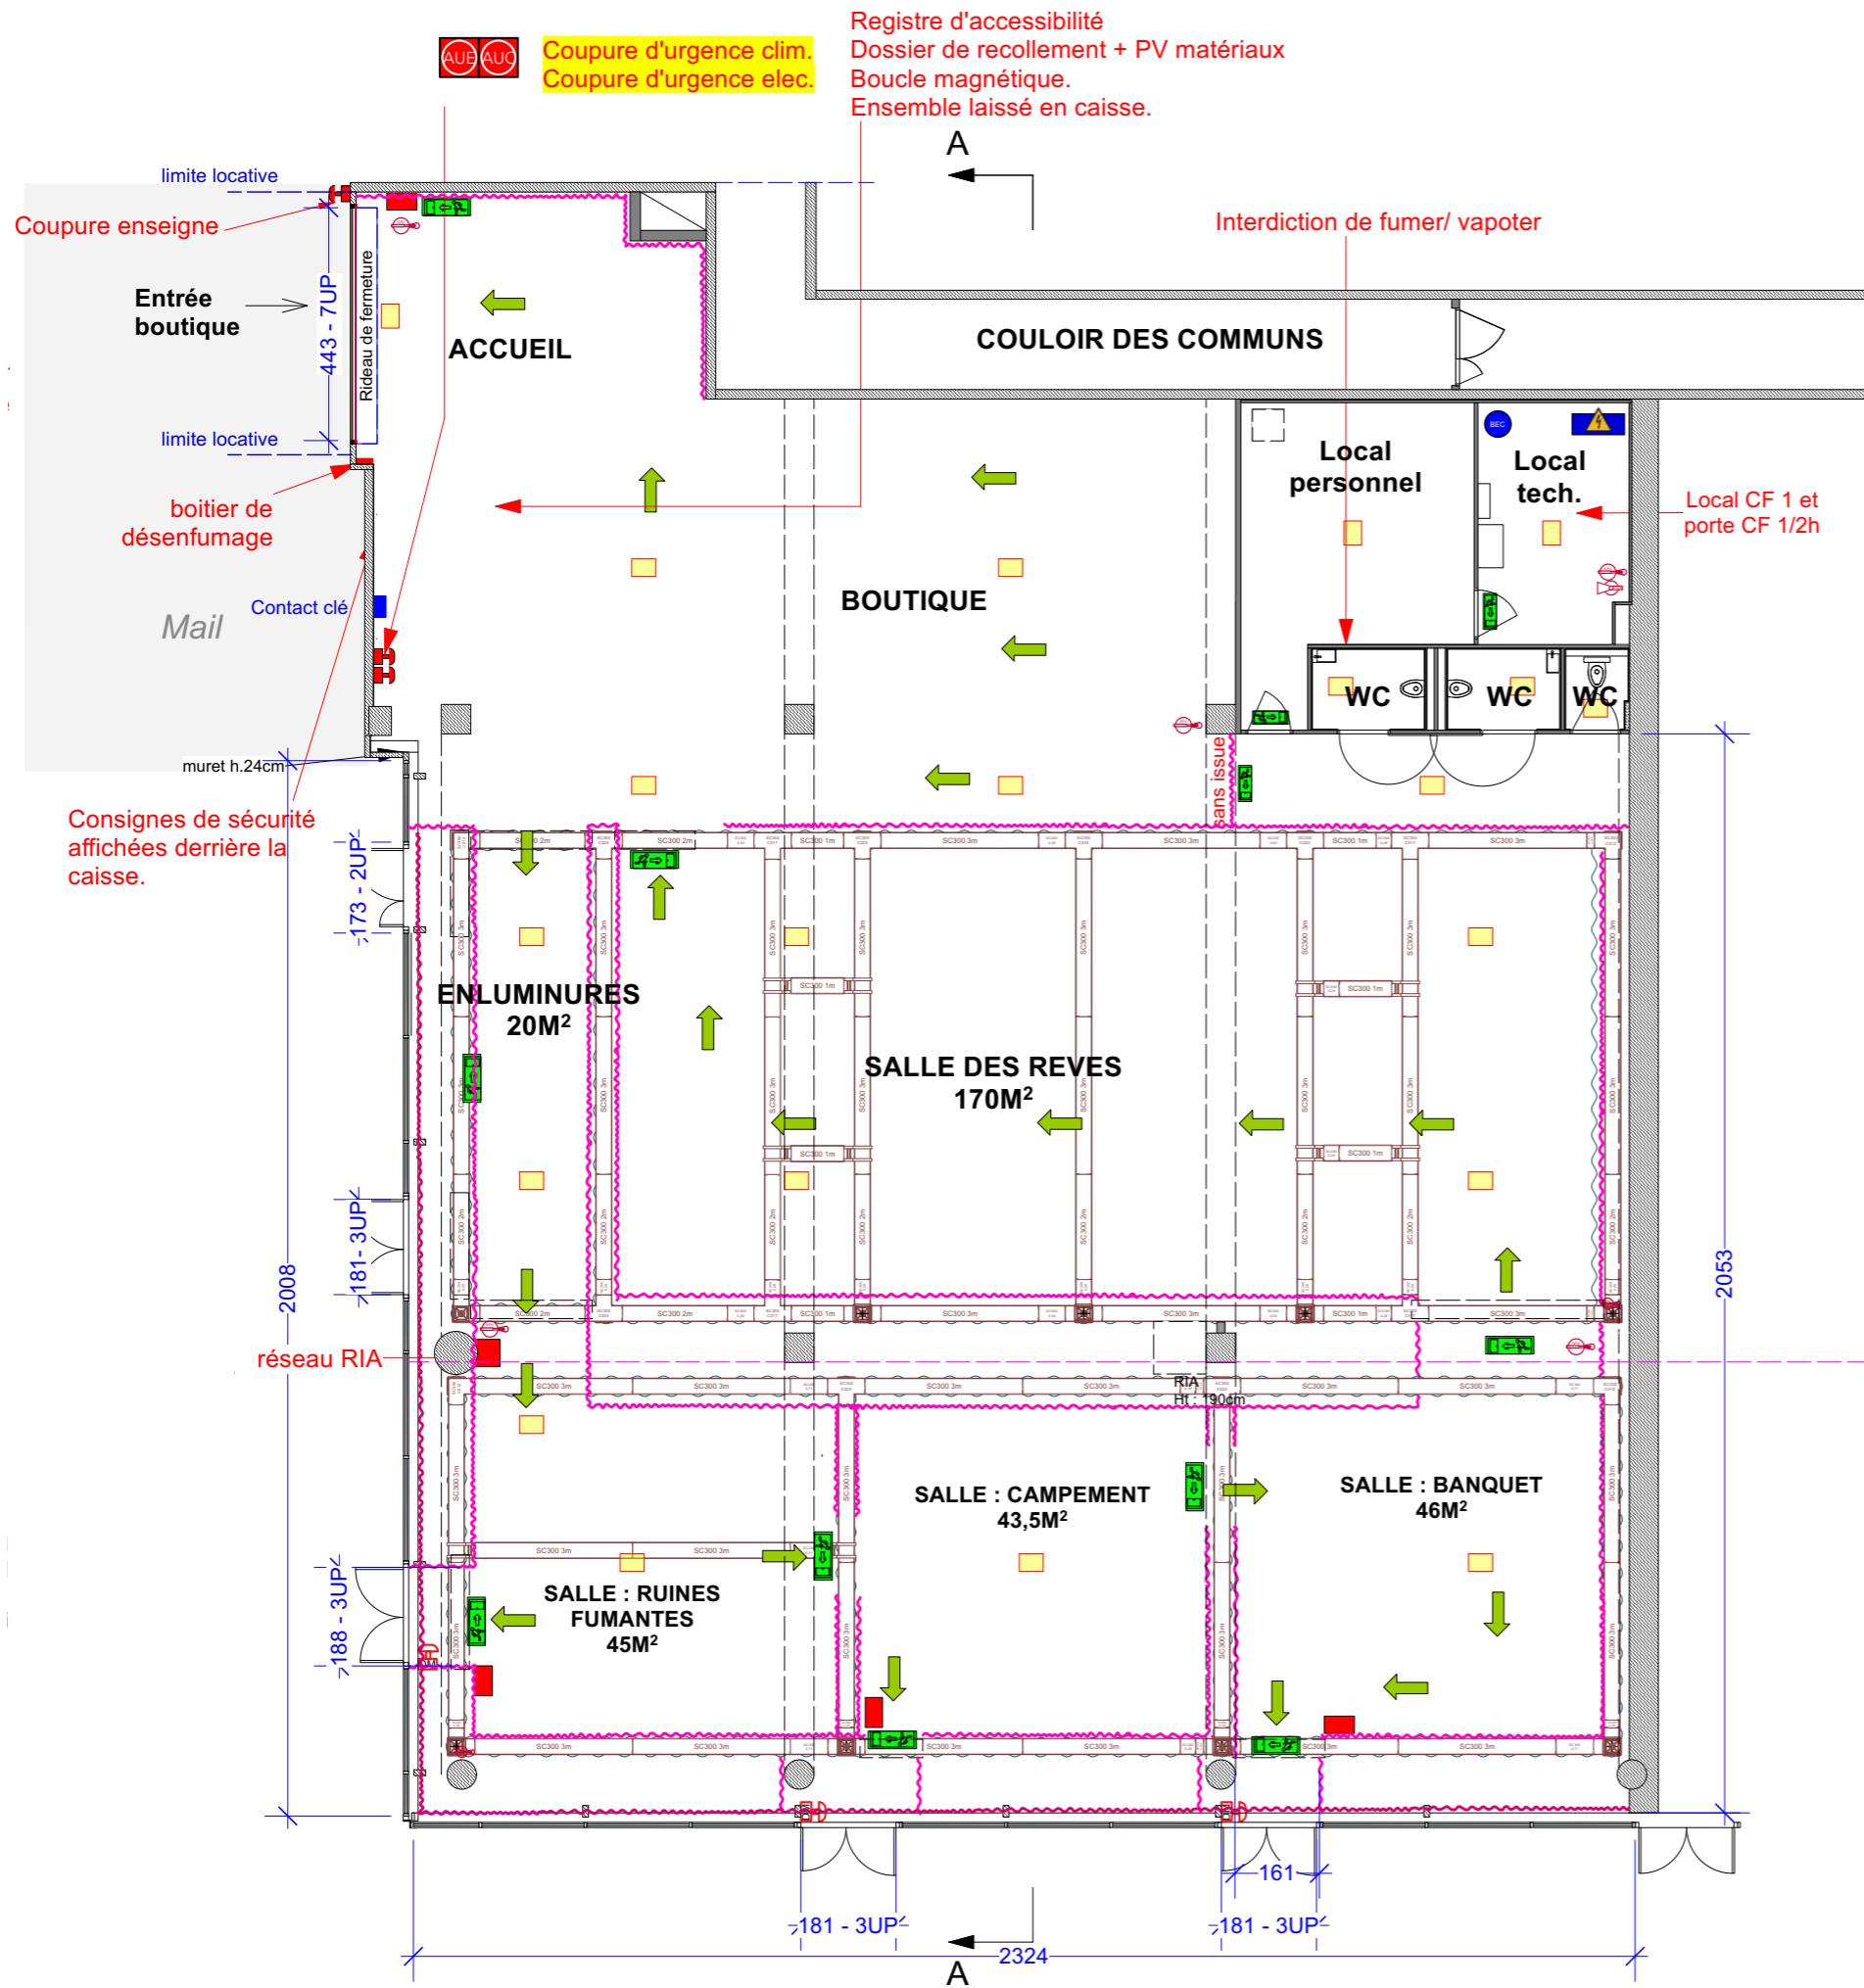

LEGENDE SECURITE



	Coupure urgence clim. Coupure électrique.
	Pictogramme "sans issue"
	Bloc de secours balisage - drapeau/ applique
	Extincteur CO2 avec signalétique
	Extincteur EP6 avec signalétique.
	Coupure d'arrêt : clim, elec et enseigne.
	Show control régie son/ lumière.
	Batterie centrale de l'éclairage de sécurité.
	Tableau électrique avec porte. Schéma unifilaire laissé dans le TE.
	Déclencheur manuel - DM
	Cheminement d'évacuation.
	Plan intervention/ évacuation consignes de sécurité.

Plan de sécurité dans le cas du dépôt
du dossier d'aménagement auprès de
la préfecture de Seine et Marne.

Rhizome

Réalisation de l'agence LNArchî

Rhizome est une péniche commerciale itinérante, parcourant un trajet de 275 km de Port-Saint-Louis à Lyon, avec 8 escales. S'inspirant des marchands ambulants d'autrefois, elle allie le « slow consuming », la coopérative équitable, l'expérience immersive et la sensibilisation au climat. À chaque escale, des producteurs locaux et leurs produits de saison montent à bord pour faire découvrir leurs produits et leur travail lors de sessions de trois heures.

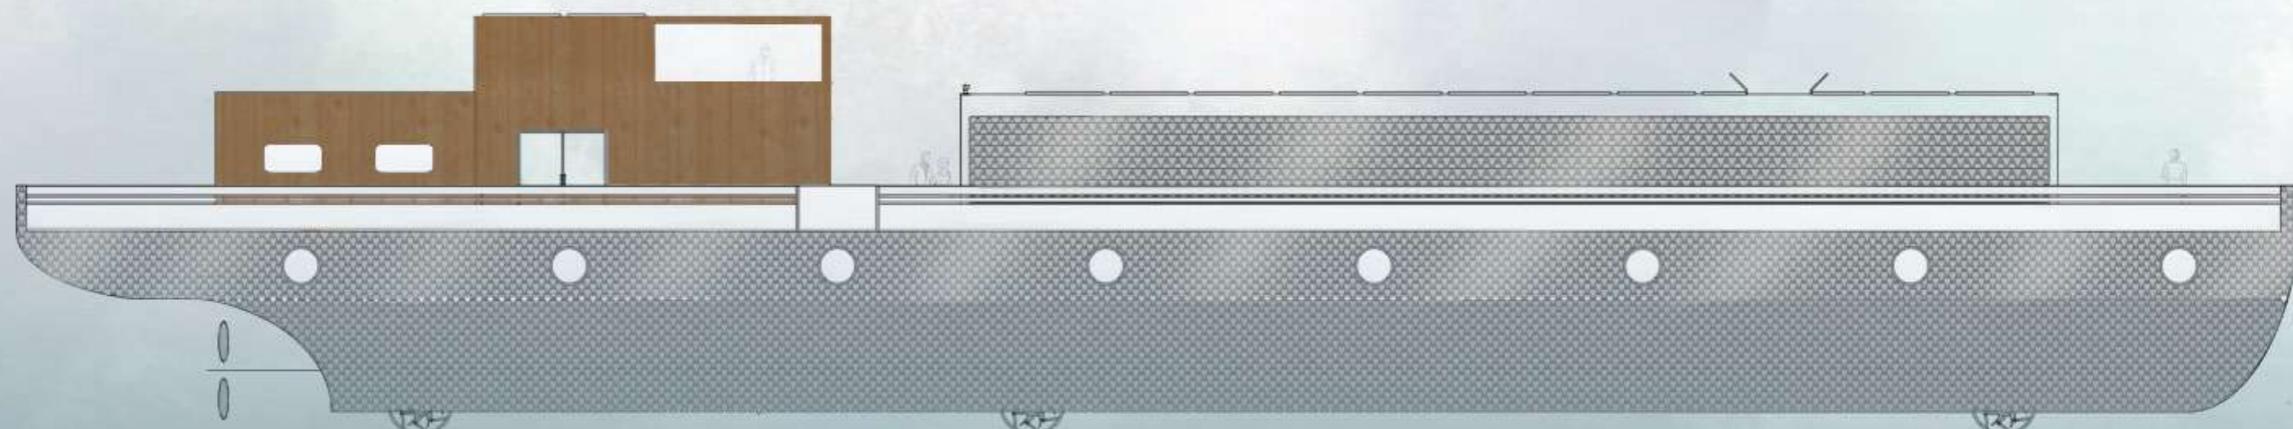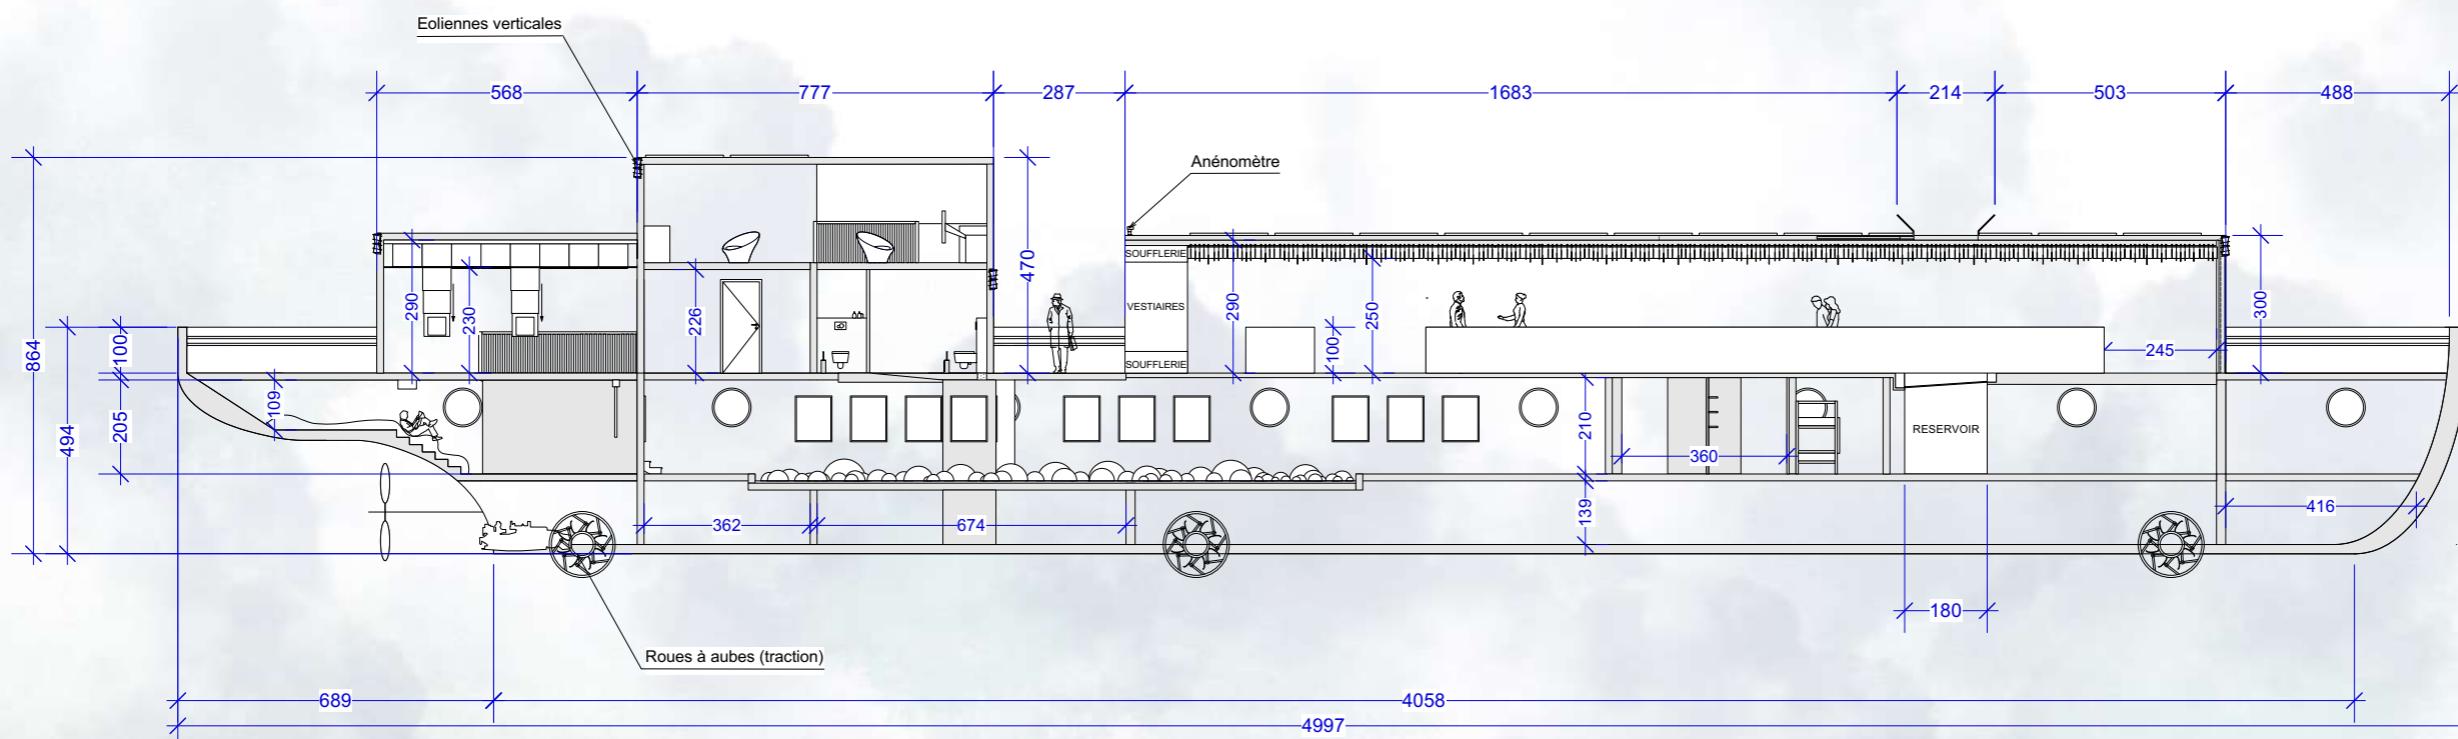




3D rendus animés

Rhizome est conçu pour s'adapter au voyage, en intégrant la météo extérieure dans son architecture afin d'améliorer le bien-être des occupants. Cette approche influence positivement leur mode de vie et leurs habitudes de consommation.


Au cœur de la scénographie intérieure, Rhizome s'ajuste aux conditions météorologiques et climatiques, créant ainsi un espace en constante évolution, avec des jeux de lumières, des ouvertures et des textures spécifiques à chaque escale.

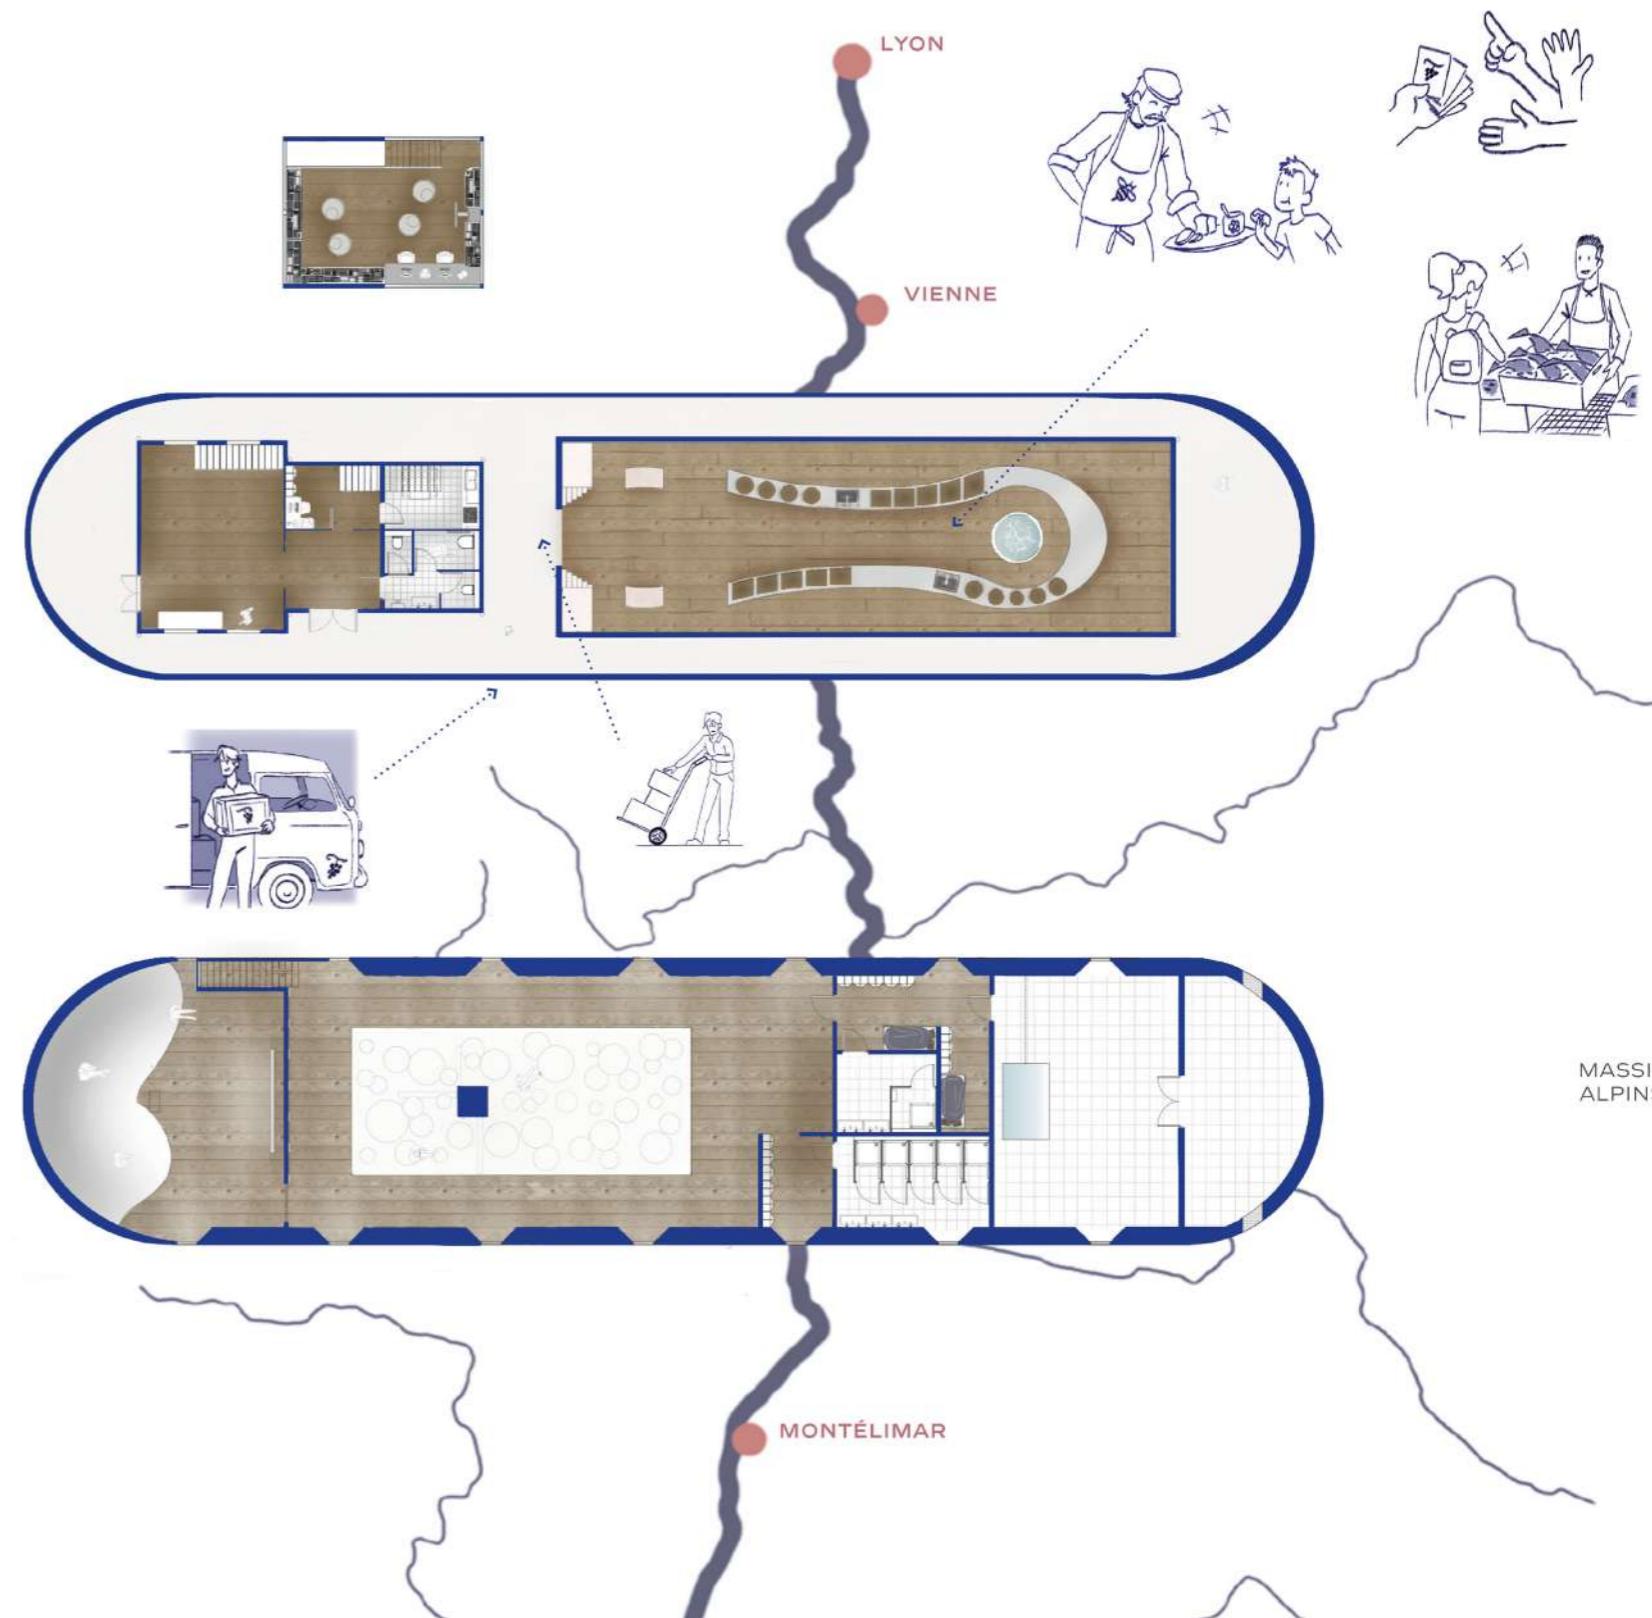


Gourmandise


Réalisé au sein de l'agence Atelier Madame

Création du dossier de consultation des entreprises pour une franchise de 400m² dédiée à un restaurant/sandwicherie. Le projet inclut une réflexion approfondie sur l'enrichissement du concept existant, en alliant la restauration rapide à une ambiance chaleureuse et accueillante. L'objectif est de créer un espace fonctionnel, moderne et convivial, tout en optimisant l'expérience client et l'efficacité du service.

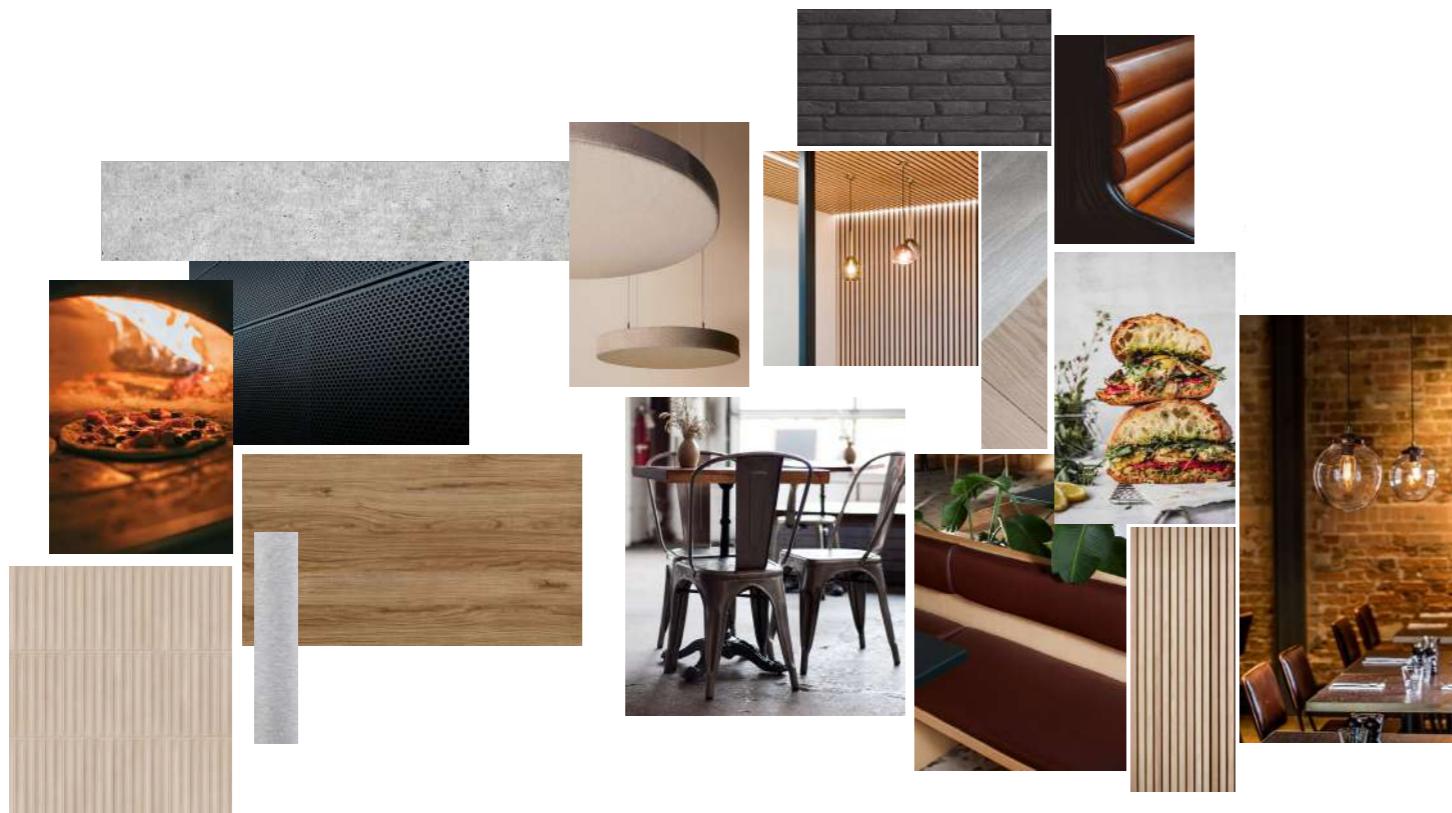

3D rendu simplifié

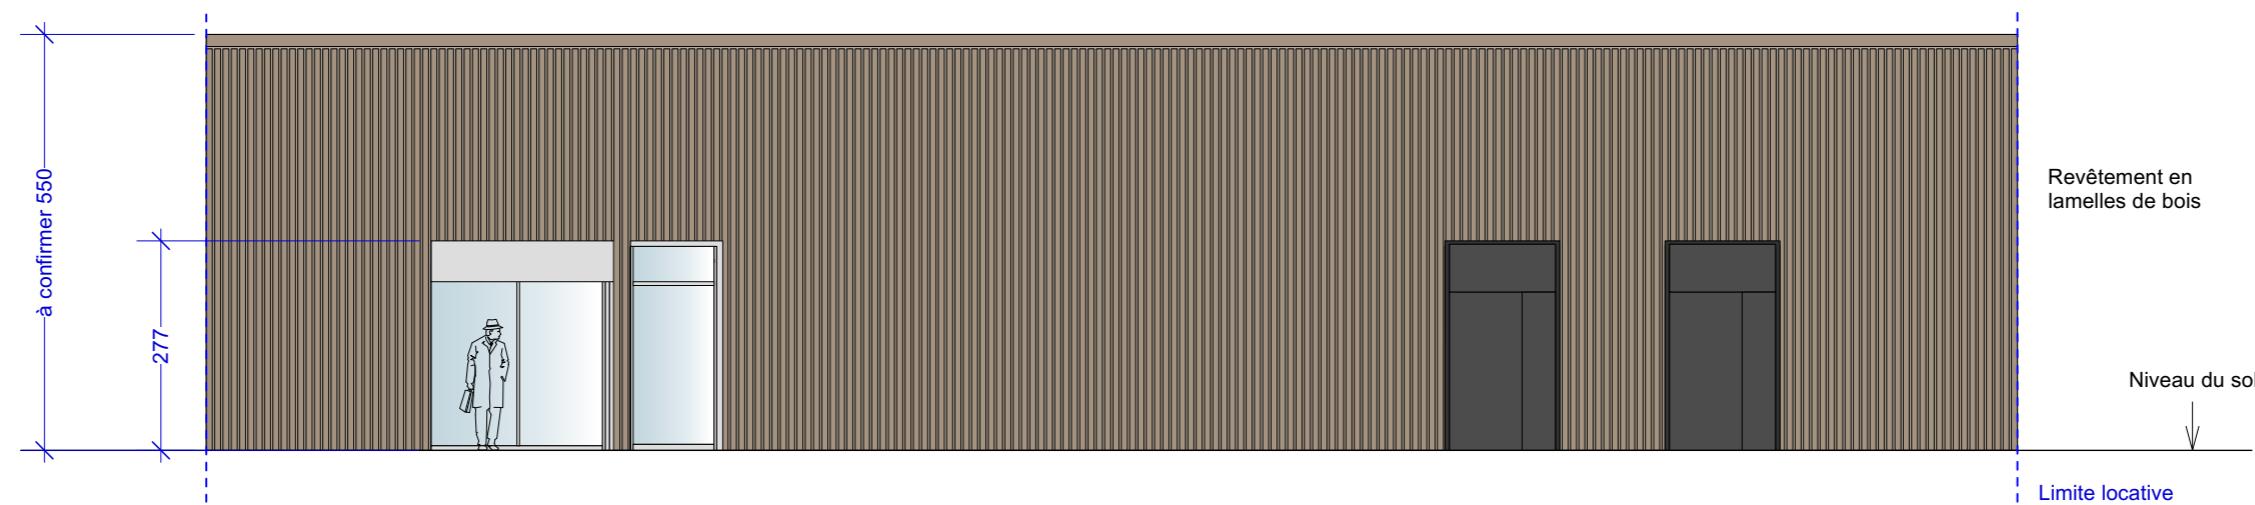

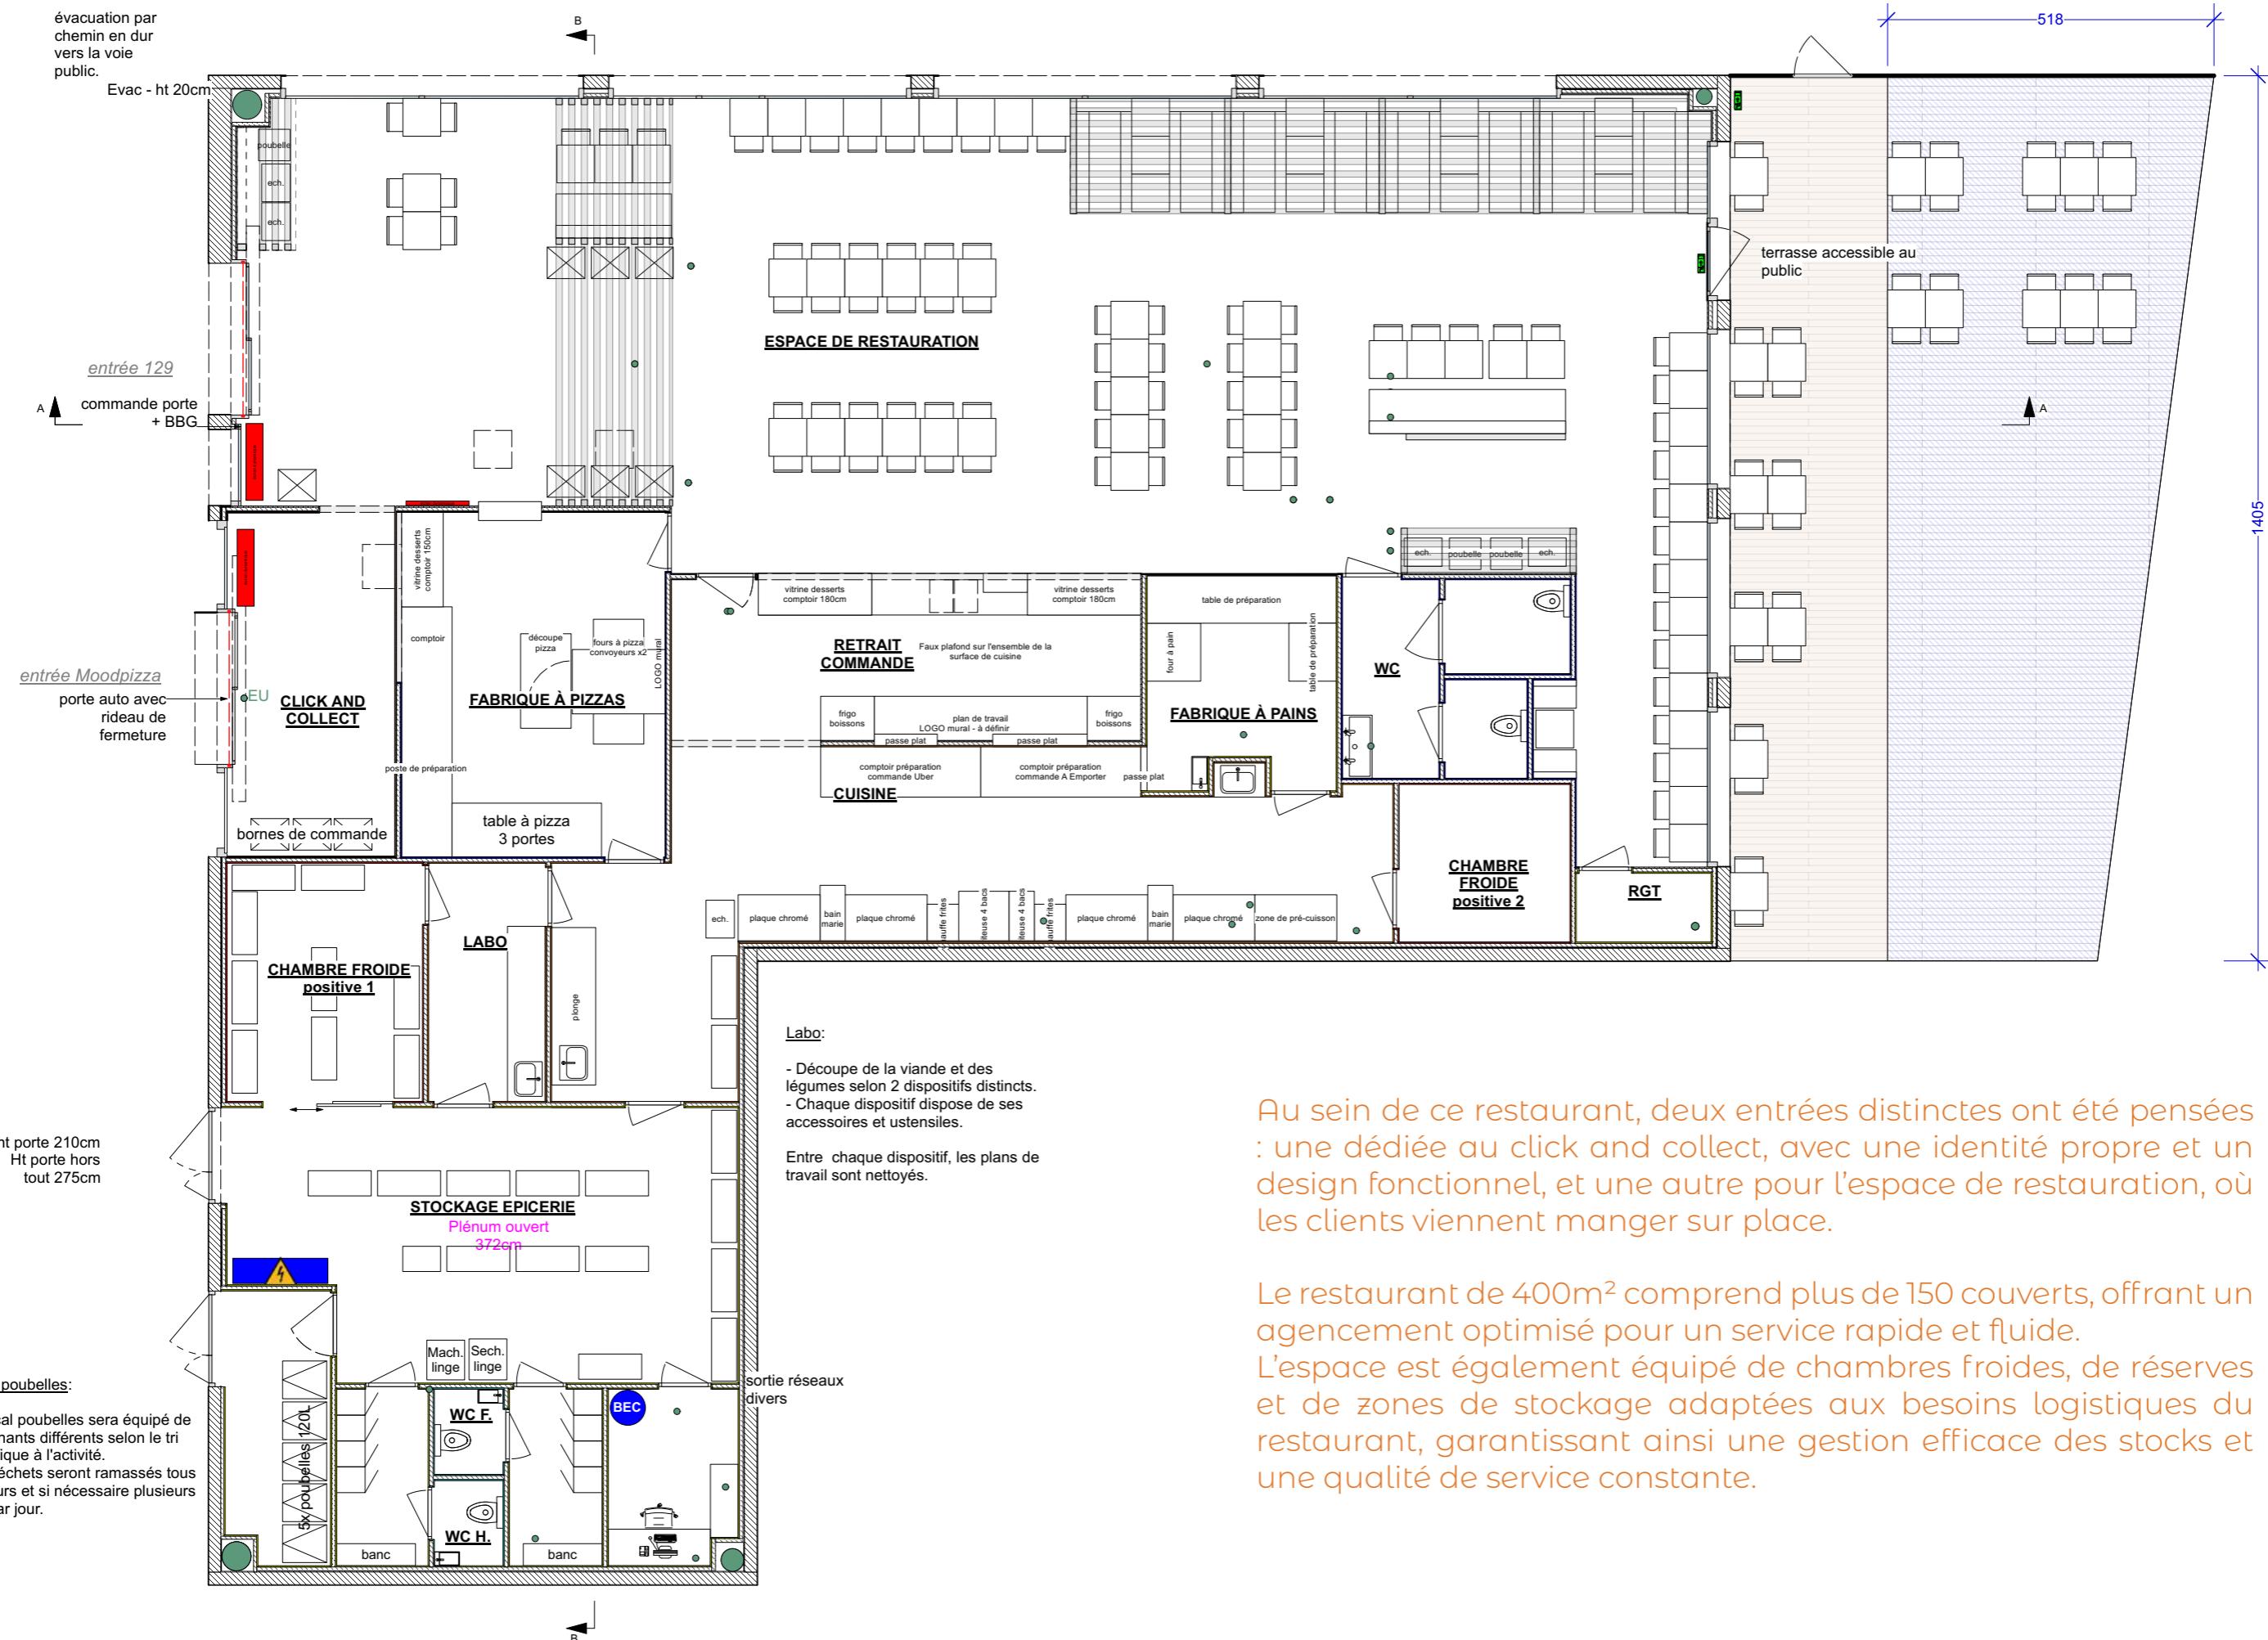

Au sein de ce restaurant, deux entrées distinctes ont été pensées : une dédiée au click and collect, avec une identité propre et un design fonctionnel, et une autre pour l'espace de restauration, où les clients viennent manger sur place.

Le restaurant de 400m² comprend plus de 150 couverts, offrant un agencement optimisé pour un service rapide et fluide. L'espace est également équipé de chambres froides, de réserves et de zones de stockage adaptées aux besoins logistiques du restaurant, garantissant ainsi une gestion efficace des stocks et une qualité de service constante.

PROCESSUS DE TRAVAIL



1. Étude préliminaire et définition du projet

Une analyse approfondie des besoins et des contraintes est réalisée afin de définir les bases du projet.

L'étude de faisabilité intègre les aspects techniques, environnementaux et réglementaires.


Un état des lieux détaillé permet d'identifier les travaux nécessaires, d'effectuer les relevés dimensionnels et d'établir une première estimation budgétaire.



2. Conception et développement créatif

Deux propositions d'aménagement sont élaborées, intégrant les exigences fonctionnelles et esthétiques du projet (APS).

Après validation d'un concept, les plans détaillés et les rendus 3D sont développés, accompagnés des précisions techniques et du choix définitif des matériaux et finitions (APD). L'ensemble des documents est finalisé et l'estimation budgétaire mise à jour (PD).

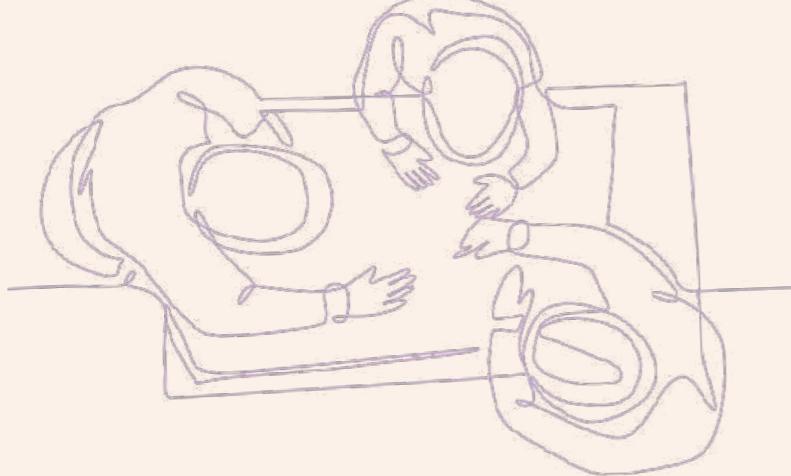

3. Planification et lancement du chantier

Un dossier technique détaillé (DCE) est établi pour consultation des entreprises et élaboration des documents contractuels. Les appels d'offres sont lancés afin de sélectionner les prestataires en cohérence avec le projet et le budget. Un planning détaillé est défini, intégrant les contraintes techniques et logistiques.



4. Suivi et coordination des travaux

Le suivi du chantier assure la conformité des travaux aux plans et aux exigences techniques. Des contrôles réguliers sont effectués, avec des ajustements en cas de contraintes imprévues. Des réunions de chantier sont organisées pour coordonner les interventions et garantir le respect des délais.



5. Réception et livraison du projet

Une visite de réception est réalisée afin de vérifier la conformité des ouvrages. Un procès-verbal de réception est ensuite signé, suivi de l'approbation des documents administratifs et financiers. Le projet est livré avec la remise du Dossier des Ouvrages Exécutés (DOE).

ILS M'ONT FAIT CONFIANCE..

LES AGENCES POUR LESQUELLES J'AI TRAVAILLÉ..



MAISON ALGA

Ponctuelle, motivée, intéressée, curieuse , elle a fait preuve de volonté de participer à chacune des missions données. Je recommande vivement et chaleureusement Hélène.



ALEXANDRA BARLUET

Helena est une personne ponctuelle, agréable, elle comprend rapidement le cahier des charges donné. Helena prend en considération les remarques qu'on lui fait, elle est motivée et aime ce qu'elle fait. Helena présente de beaux rendus graphiques.



ATELIER MADAME

Dans le cadre du développement de l'agence, nous avons recruté Hélène, afin de nous accompagner sur les missions de maîtrise d'œuvre comprenant la réalisation de plans et de dossiers administratifs ainsi que l'élaboration de concept retail. Hélène a rempli parfaitement ses missions, faisant preuve de détermination, de curiosité et d'implication. C'est à regret que nous nous séparons d'Hélène, mais sommes convaincus qu'elle a beaucoup à apporter à une autre entreprise, tant par son professionnalisme que sa personnalité dynamique.

LES RETOURS DE MES CLIENTS..



PROJET SAINTE MARIE

Nous avons fait appel à Hélène pour repenser notre salle à manger, notre cuisine et une chambre, et nous sommes absolument ravis du résultat. Elle a su faire preuve d'un grand professionnalisme, en nous proposant des idées créatives et adaptées à nos besoins. Son travail soigné et son sens du détail ont fait toute la différence. Nous la recommandons sans hésitation !



PROJET DOUDEVILLE

Très bonne professionnelle à l'écoute et ayant de très bonnes idées. Belles réalisations d'aménagement de notre salon. Nous recommandons.



PROJET BRAS D'OR

Un immense merci à LNArchi, pour la rénovation de mon rez de chaussée ! Isolation, électricité, aménagement du salon, de la salle à manger et des WC : tout a été réalisé avec soin et professionnalisme. Grâce à votre talent et votre écoute, mon intérieur est transformé. L'ambiance est désormais chaleureuse et harmonieuse et exactement comme je l'avais imaginée. Je me sens vraiment chez moi ! Merci encore pour ce magnifique travail !





CONTACT

Si vous avez des questions, des propositions de collaboration ou des demandes de projet, n'hésitez pas à me contacter ! Je serais ravie de discuter avec vous.

Email : h.grebeauval@lnarchi.com

Téléphone : 06 52 12 25 17

LinkedIn : www.linkedin.com/in/helenagrebeauval

Site Web : lnarchi.com

Instagram : @lnarchi.interieur

